


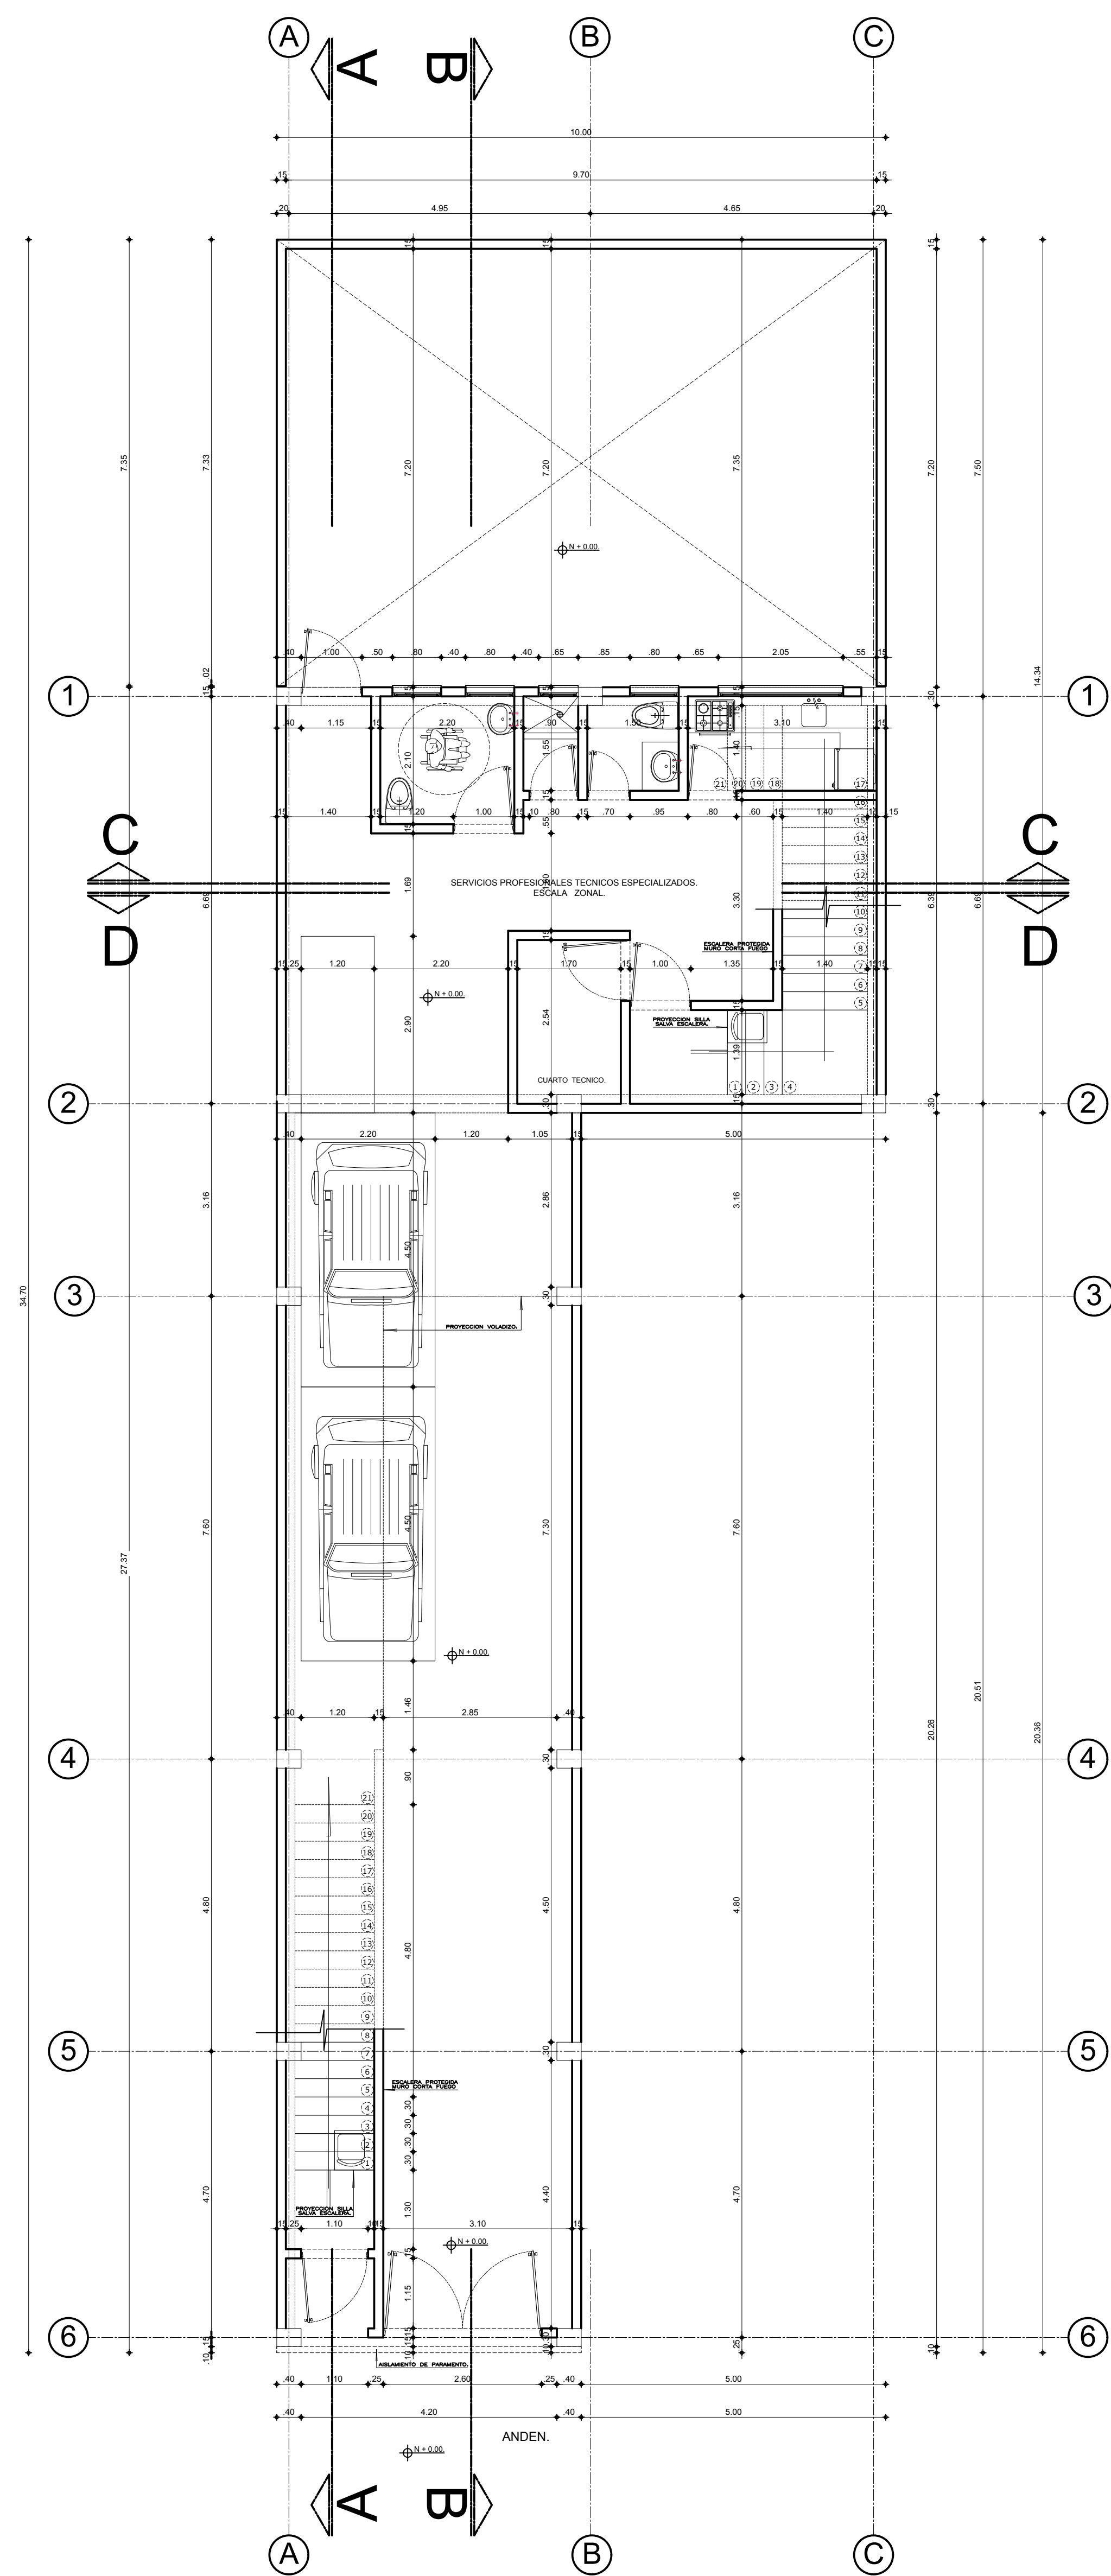

PLANTA PISO 1.
ESCALA : 1 : 50.

CUADRO DE AREAS.

DESCRIPCION.	AREA CONSTRUIDA.	AREA DESCUENTO I.C.	AREA CALCULO I.C.
AREA DE LOTE	245.14 M2		
AREA CONSTRUIDA PISO 1	171.14 M2	130.24 M2	40.90 M2
AREA CONSTRUIDA PISO 2	105.45 M2	46.65 M2	58.80 M2
AREA TOTAL CONSTRUIDA	276.59 M2	176.89 M2	99.70 M2
AREA LIBRE PISO 1.	74.00 M2		


CUADRO DE ESTACIONAMIENTOS Y BICICLETAS.

SECTOR DE DEMANDA B (AREA PARA CALCULO DE PARQUEADEROS: 99.70 M2).

VIVIENDA.	EXIGIDOS.	PROPUESTOS.
PRIVADOS : 1 x CADA 40 M2 / 2.	1	2
VISITANTES: 1 x CADA 50 M2 / 2.	0	0
BICICLETAS: 1 X C/2 PARQUEADEROS.	0	1

CUADRO DE INDICES.

INDICES.	EXIGIDOS.		PROPUESTOS.	
INDICE DE OCUPACION: 245.14 M2 x .70.	70 %	171.60 M2.	69 %	171.14 M2.
INDICE DE CONSTRUCCION: 245.14 x 2.5.	2.5 %	612.85 M2.	1.13 %	276.59 M2.

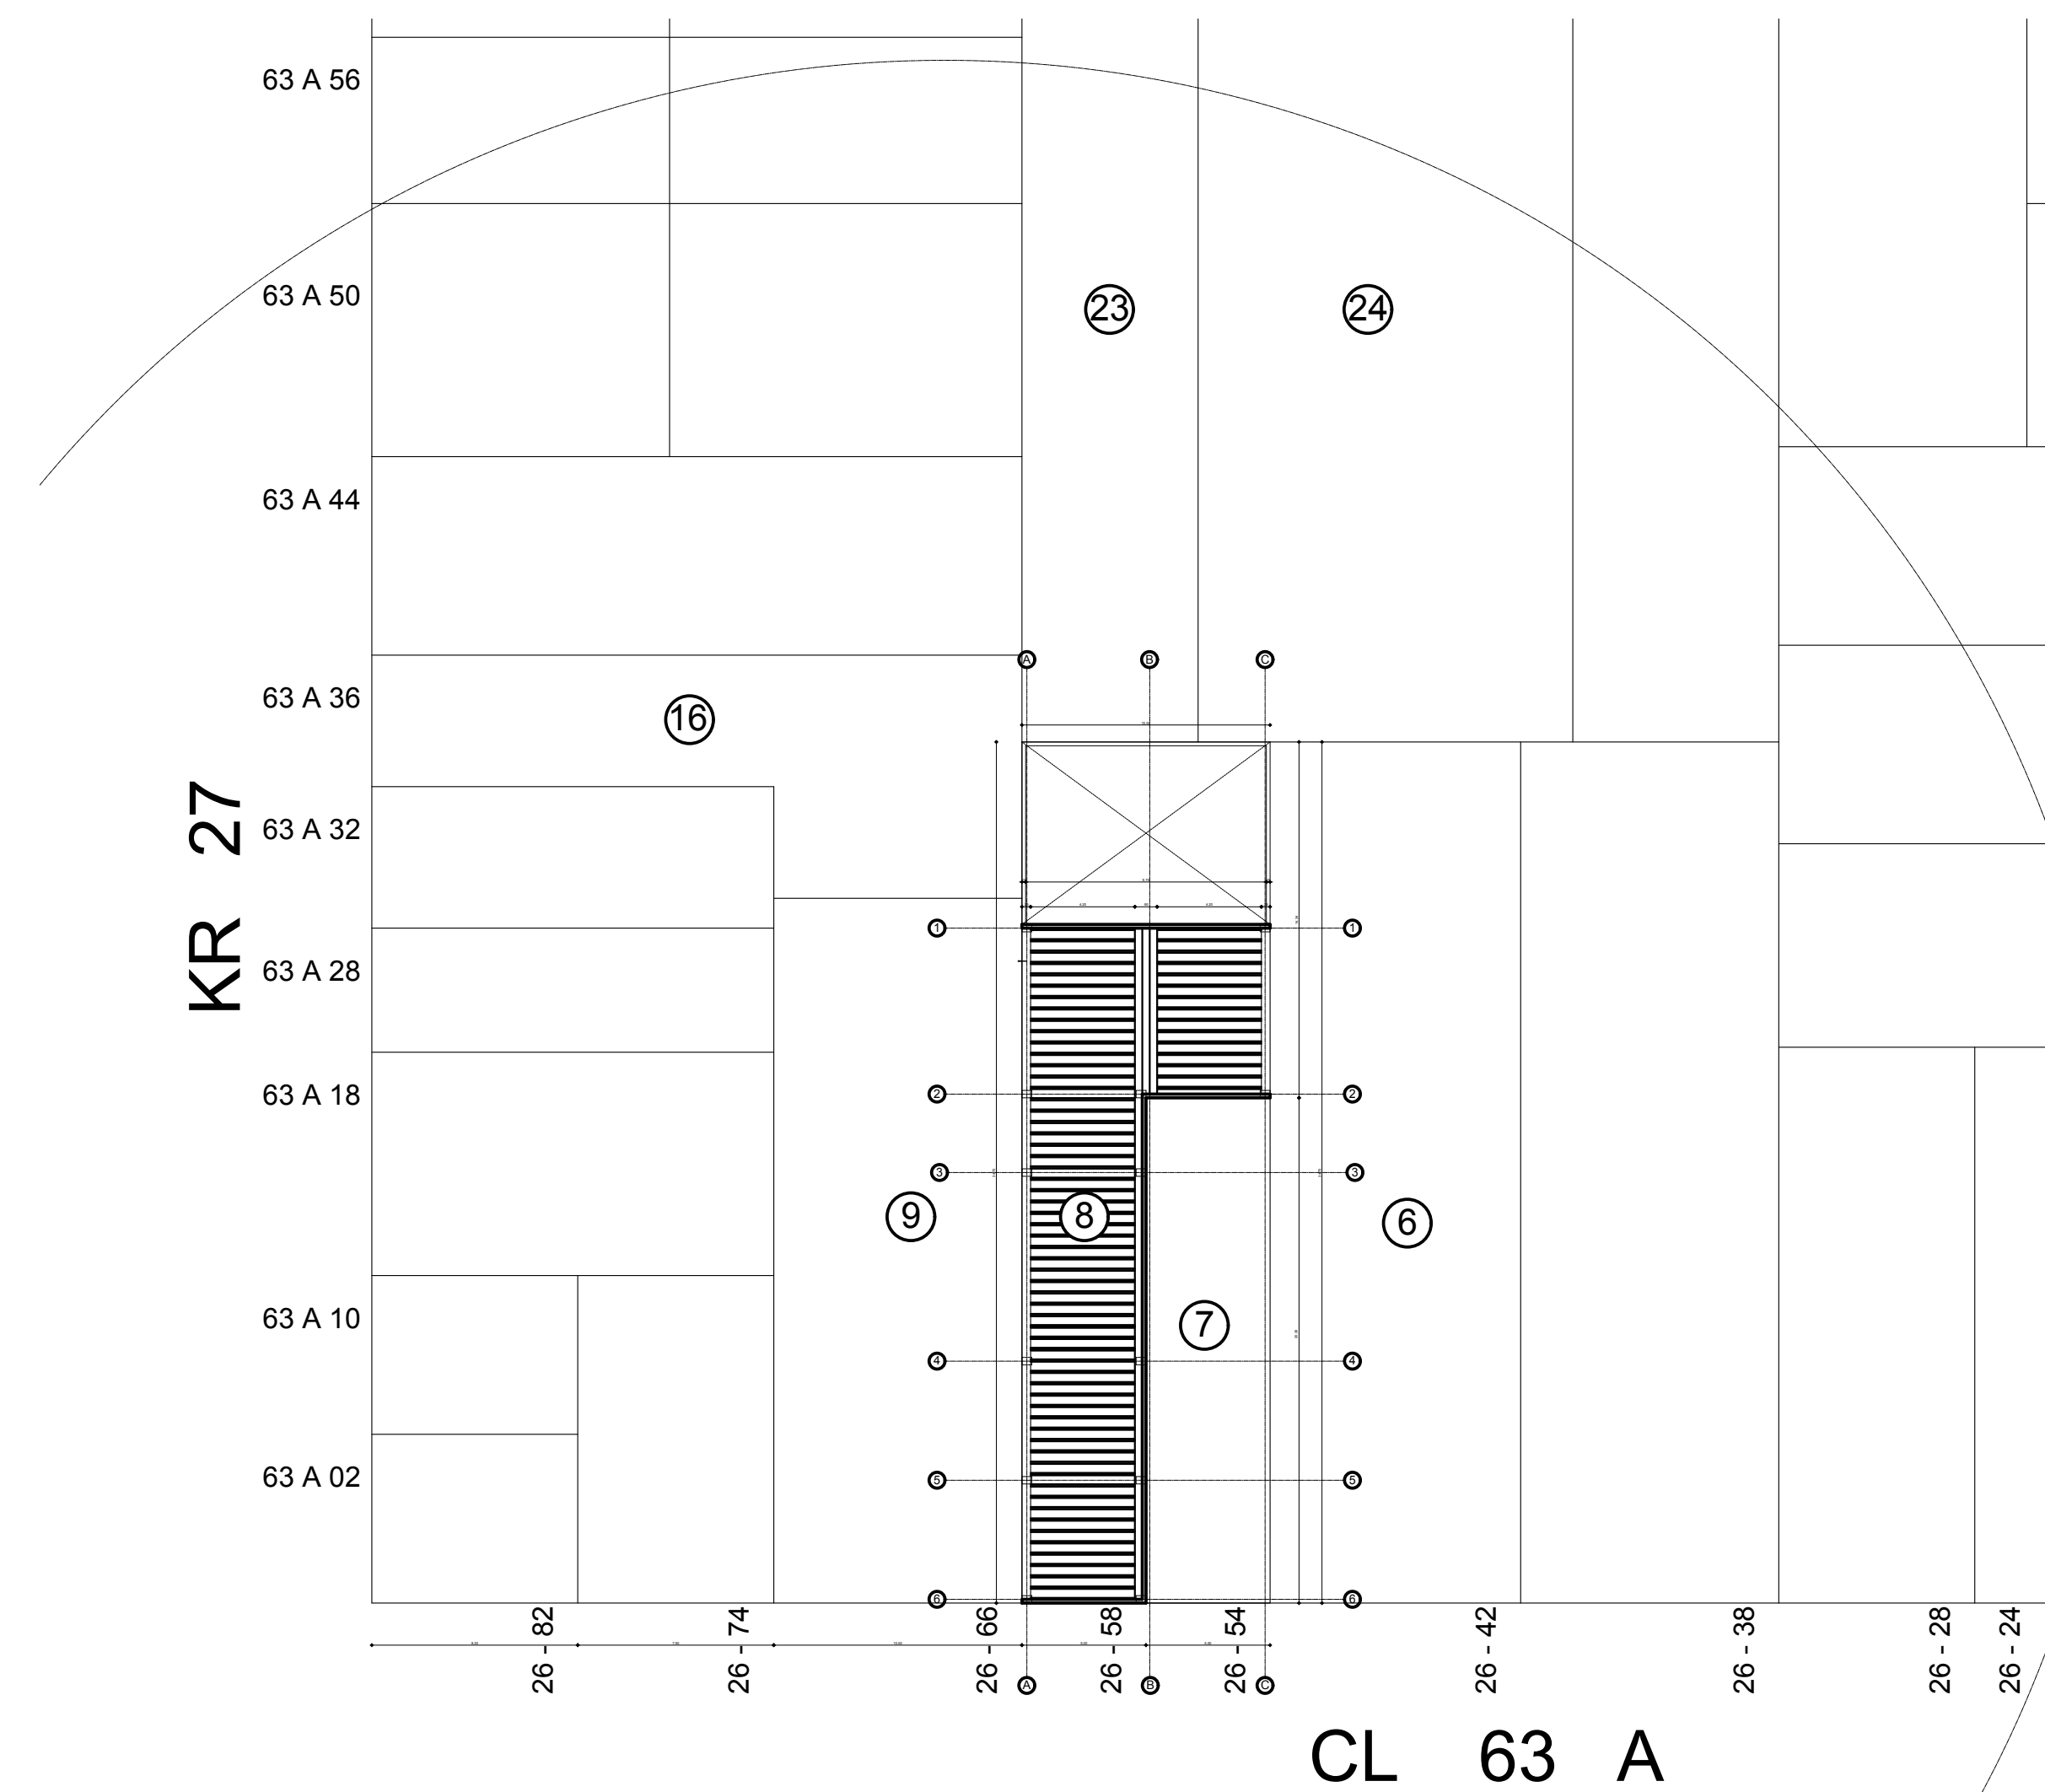

LOCALIZACION.



PROYECTO:
**BODEGA
ALCAZARES.**

UBICACION:
CALLE 63 A # 26 - 58.
Barrio Quinta Mutis - Bogotá D.C.

Vo. Bo. PROPIETARIO:


MAGDA RODRIGUEZ. CC. 51.837.672 BOGOTÁ
PATRICIA RODRIGUEZ. CC. 51.777.474 BOGOTÁ.

CONSTRUYE:

CONTIENE
**PLANTA PRIMER PISO.
CUADRO DE AREAS.
LOCALIZACION.**

ARQUITECTO RESPONSABLE:

ARQ. JUAN CARLOS GARZON PEDRAZA
MAT. PROF. 25700-37516 CND

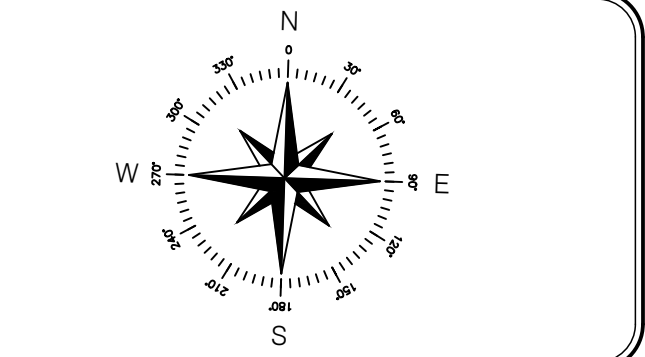

REVISO:

OBSERVACIONES:

SELLOS DE APROBACION:

DISEÑO Y ACTUALIZACIONES:

DIGITO: Semith Tboada email: sstaboada@gmail.com

LÍNEA DE ACCESO D:\Arquitectos\301_acad_files\arquitectonicos\Arq_ICGarzon\planos\17112_26-29-Arq_Fmt_Planos\17-26.dwg

PLUMAS PARA PLOTEAR


Color	Nº	Nº	Nº	Nº	Color	Nº	Nº	Nº	Color	Nº	Nº	Nº
Red	7	0.15	10	7	0.15	10	7	0.15	10	7	0.15	10
Yellow	7	0.20	10	7	0.20	10	7	0.20	10	7	0.20	10
Green	7	0.30	10	7	0.30	10	7	0.30	10	7	0.30	10
Cyan	7	0.40	10	7	0.40	10	7	0.40	10	7	0.40	10
Blue	7	0.50	10	7	0.50	10	7	0.50	10	7	0.50	10
Magenta	7	0.60	10	7	0.60	10	7	0.60	10	7	0.60	10
Black	7	0.70	10	7	0.70	10	7	0.70	10	7	0.70	10
White	7	0.80	10	7	0.80	10	7	0.80	10	7	0.80	10

FECHA
21-02-2017


ESCALA
1:50

PLANO No.
A1

DE : 04

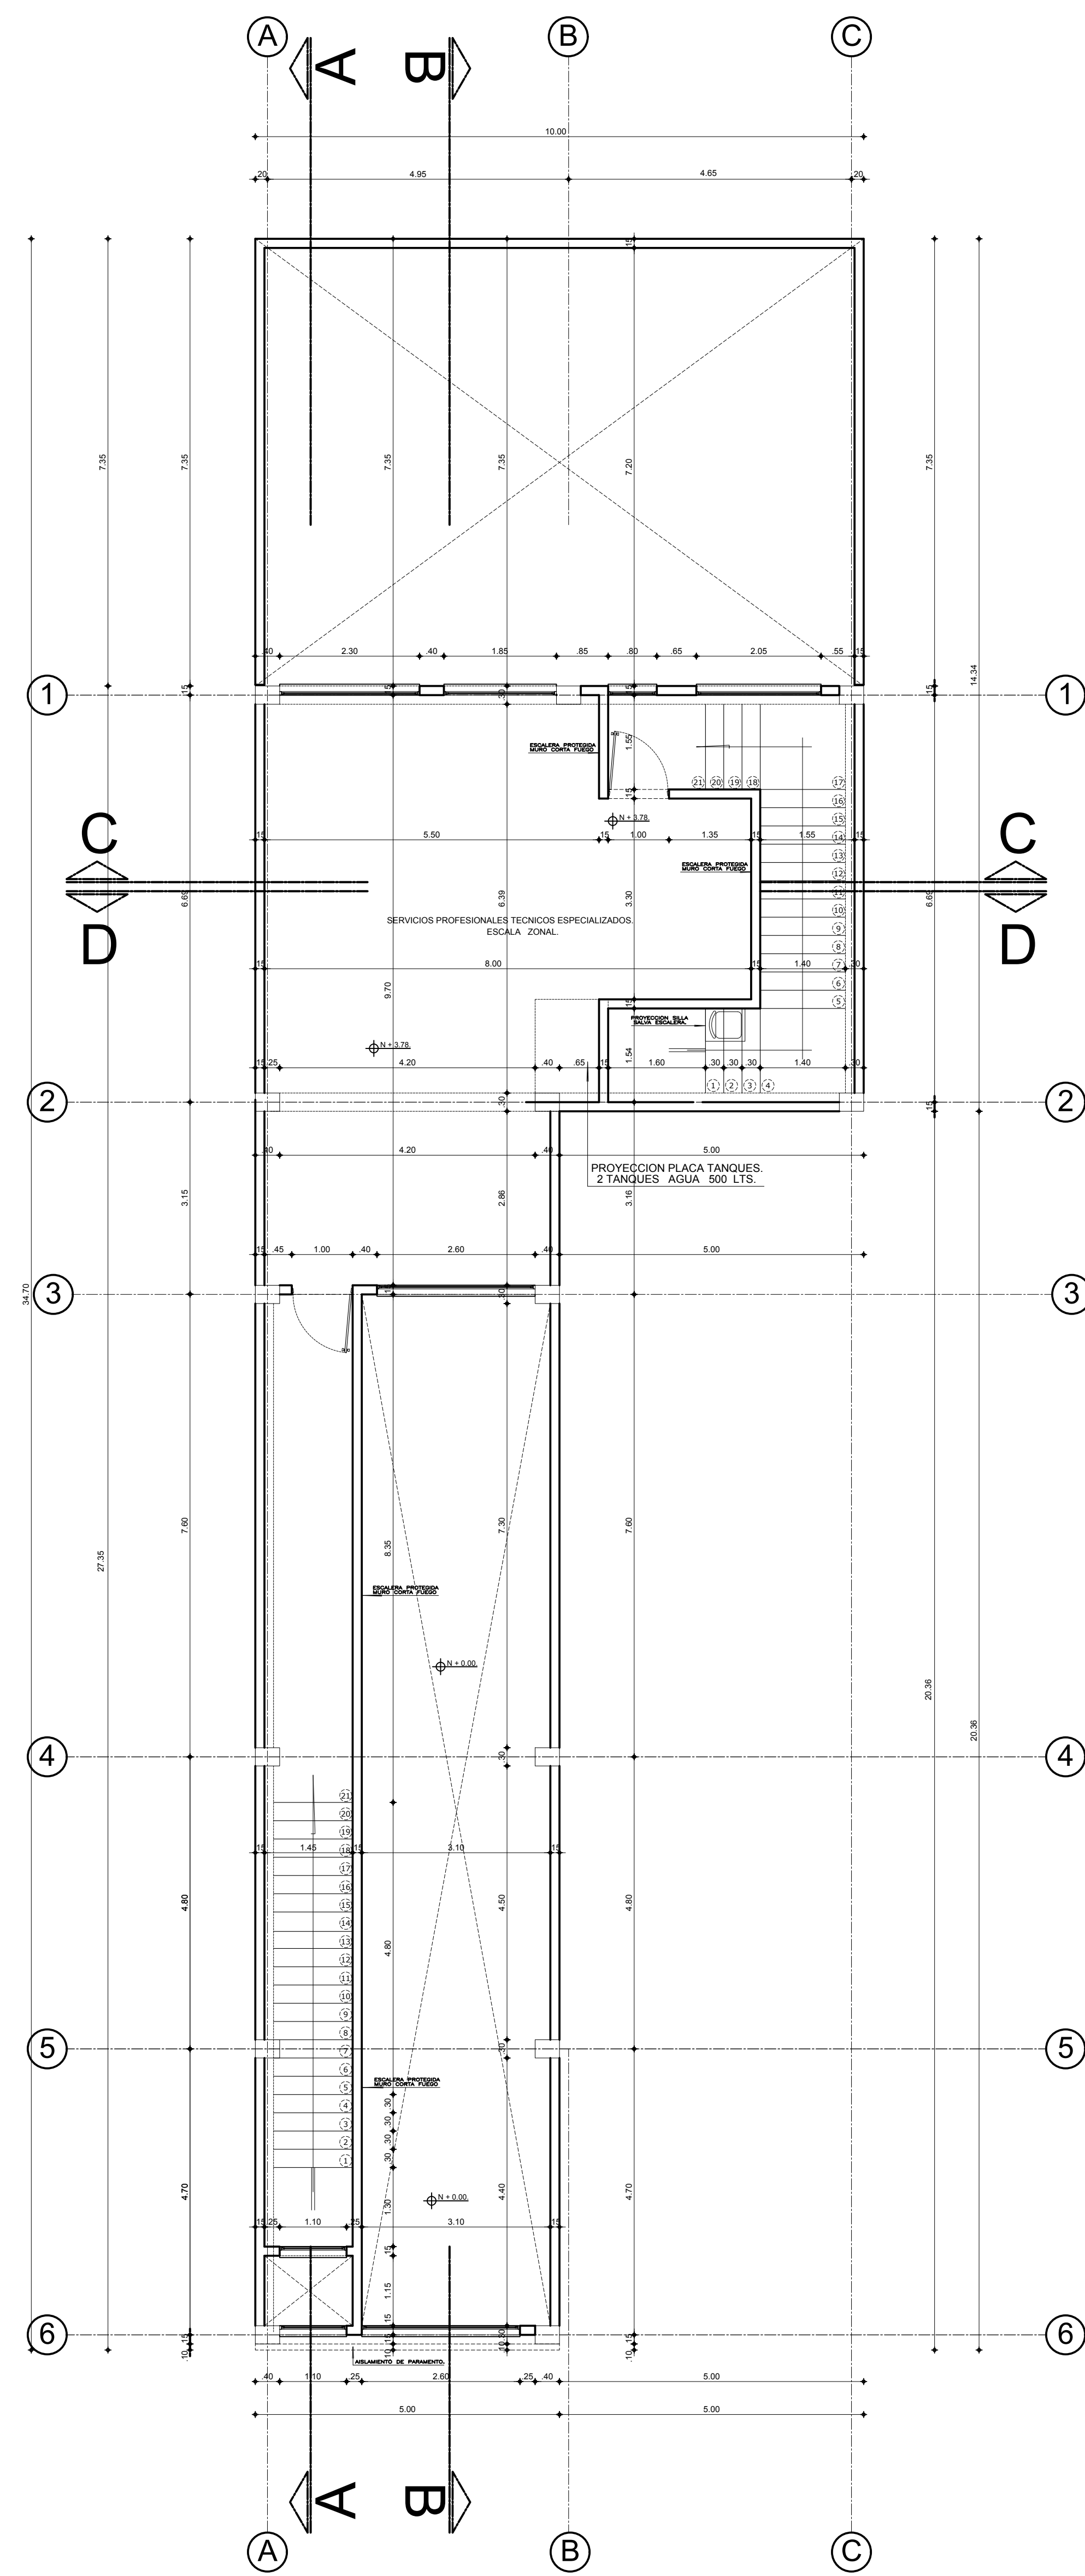

PLANTA PISO 2.
ESCALA : 1 : 50.

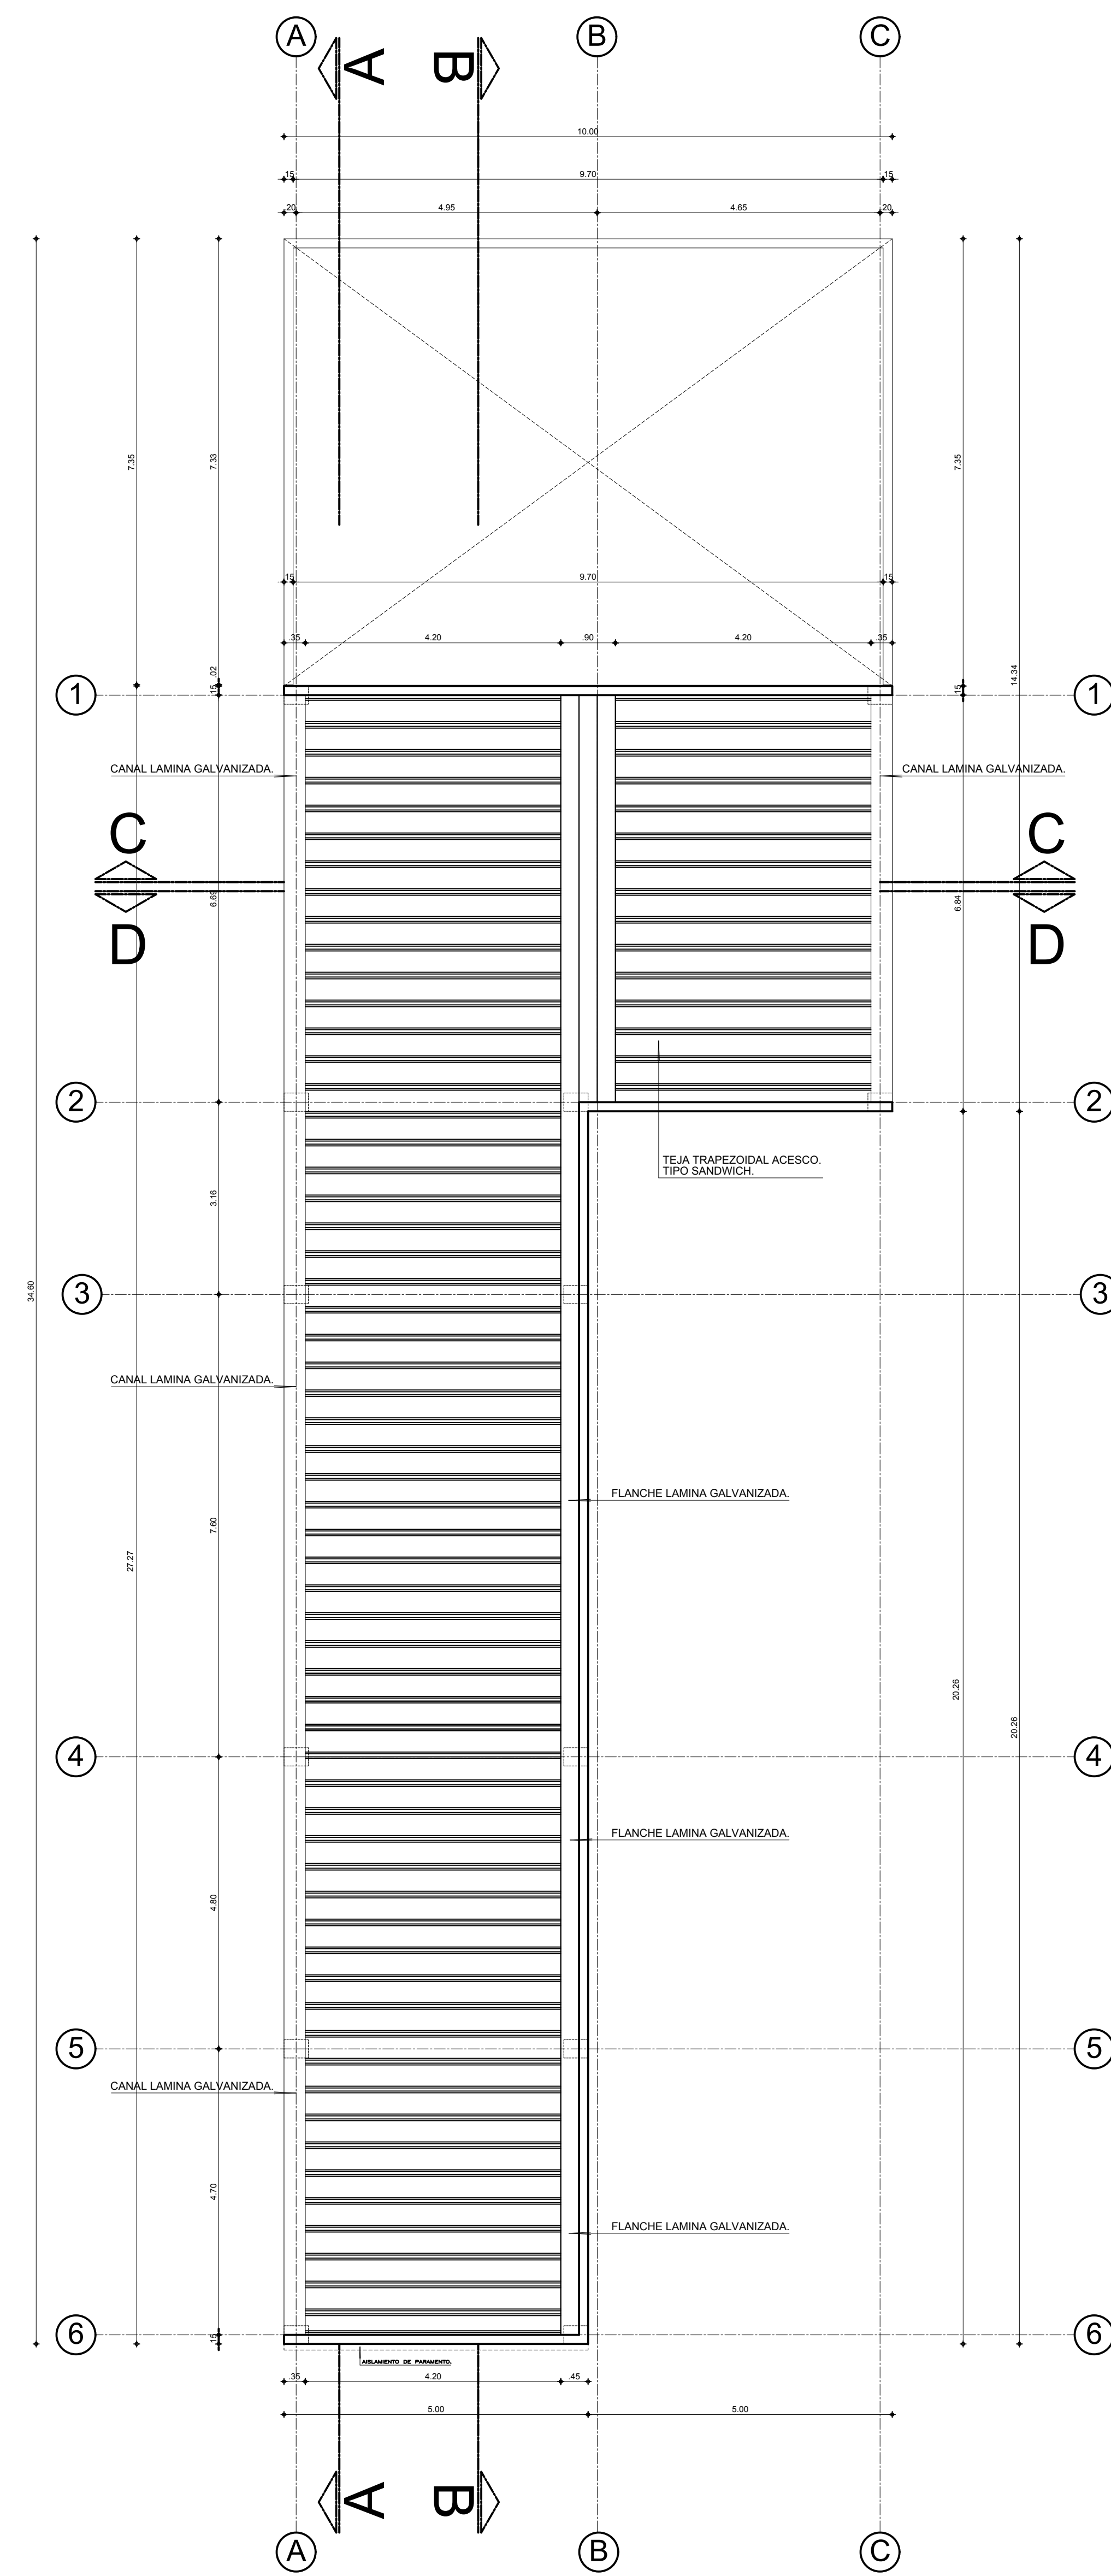

PLANTA DE CUBIERTAS.
ESCALA : 1 : 50.



PROYECTO:
**BODEGA
ALCAZARES.**

UBICACION:
CALLE 63 A # 26 - 58.
Barrio Quinta Mutis - Bogotá D.C.


Vo. Bo. PROPIETARIO:

MAGDA RODRIGUEZ. PATRICIA RODRIGUEZ.
CC. 51.837.672 BOGOTÁ CC. 51.777.474 BOGOTÁ.

CONSTRUYE:

CONTIENE
**PLANTA PISO 2.
PLANTA DE CUBIERTAS.**

ARQUITECTO RESPONSABLE:
ARQ. JUAN CARLOS GARZON PEDRAZA
MAT. PROF. 25700-37516 CND

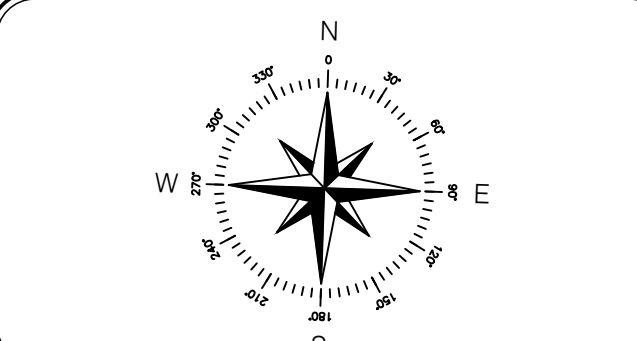

REVISO:

OBSERVACIONES:

SELLOS DE APROBACION:

DISEÑO Y ACTUALIZACIONES:

DIGITO: Semith Tboada email: sstaboada@gmail.com

LÍNEA DE ACCESO D:\Arquitectura\301_acad_files\arquitectonicos\...

P L U M A S P A R A P I O T E A R			
Color	Nº	Nº	Nº
Rojo	1	1.15	1.15
Verde	2	0.20	1.00
Azul	3	0.20	1.00
Naranja	4	0.20	1.00
Grises	5	0.20	1.00
Blanco	6	0.20	1.00
Negro	7	0.20	1.00
Otros	8	0.20	1.00

FECHA: 21-02-2017
PLANO No. **A2** DE: 04
ESCALA: 1:50

PROYECTO:

**BODEGA
ALCAZARES.**

UBICACION:

CALLE 63 A # 26 - 58.
Barrio Quinta Mutis - Bogotá D.C.

Vo. Bo. PROPIETARIO:

MAGDA RODRIGUEZ
CC. 51.837.672 BOGOTÁ

PATRICIA RODRIGUEZ
CC. 51.777.474 BOGOTÁ.


CONSTRUYE:

CONTIENE

CORTE LONGITUDINAL A - A.
CORTE LONGITUDINAL B - B.
CORTE TRANSVERSAL C - C.
CORTE TRANSVERSAL D - D.

ARQUITECTO RESPONSABLE:

ARG. JUAN CARLOS GARZON PEDRAZA
MAT. PROF. 25700-37516 CND

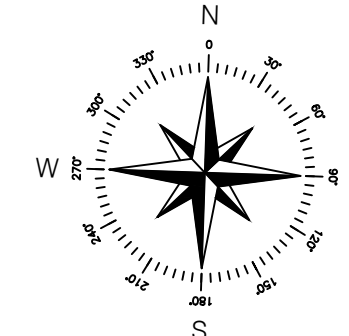

REVISO:

OBSERVACIONES:

SELLOS DE APROBACION:

DIGITO: Samith Taboada email: sstaboada@gmail.com

LÍNEA DE ACCESO D:\Arquitectos\24h_acad_files\Arquitectos\Arg_JC\GarzonPedraza_137012_198-20_Plan_24h_Planos\137-24h.dwg

PLUMAS PARA PLOTTEAR											
Color	Pen No.	Pen Width	Color	Pen No.	Pen Width	Color	Pen No.	Pen Width	Color	Pen No.	Pen Width
Black	7	0.15	Red	7	0.3	Blue	104	7	0.05		
Yellow	7	0.20	Green	7	0.15	White	120	7	0.45		
Cyan	7	0.30	Magenta	11	7	0.30	Light Blue	120	7	0.30	
Gray	7	0.40	Dark Blue	15	7	0.15	Dark Green	140	7	0.25	
Blue	7	0.50	Dark Red	180	7	0.10	Dark Magenta	253	7	0.15	
Magenta	7	0.60	Dark Cyan	44	7	0.10	Dark Yellow	294	7	0.10	
Red	7	0.10	Dark Blue	45	7	0.45	Dark Green	30	7	0.15	
Green	7	0.80	Dark Red	50	7	0.15					







FECHA
22-12-2016

ESCALA
1:50

PLANO No.

A3

DE: 04

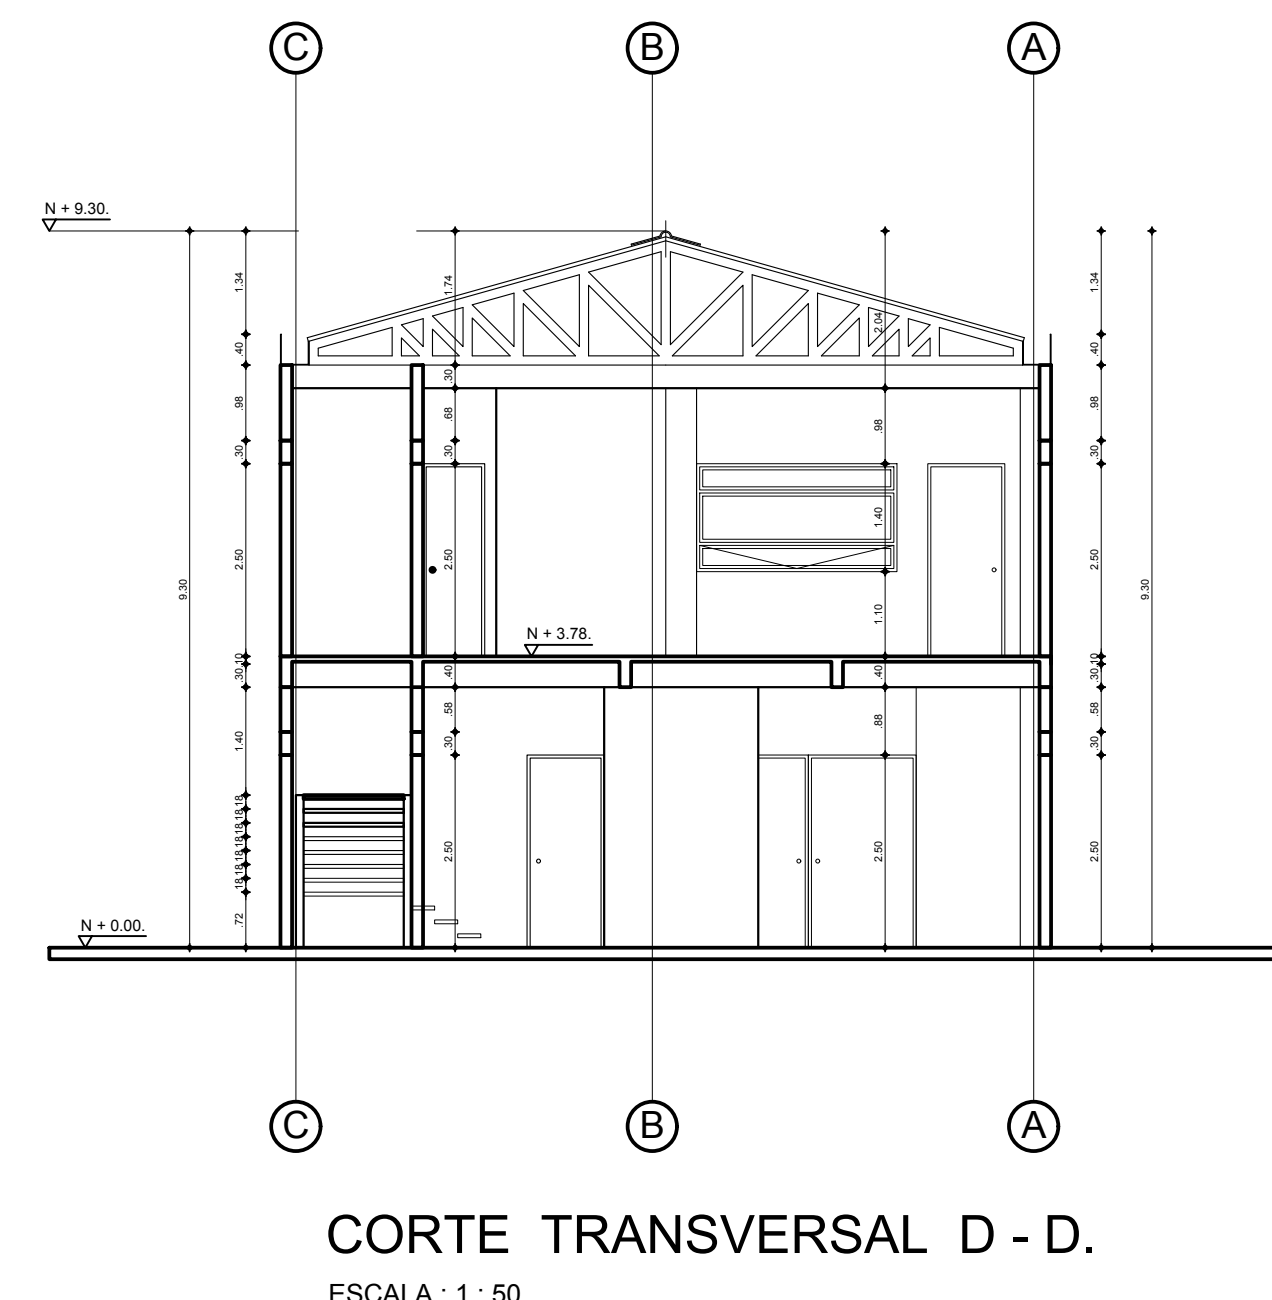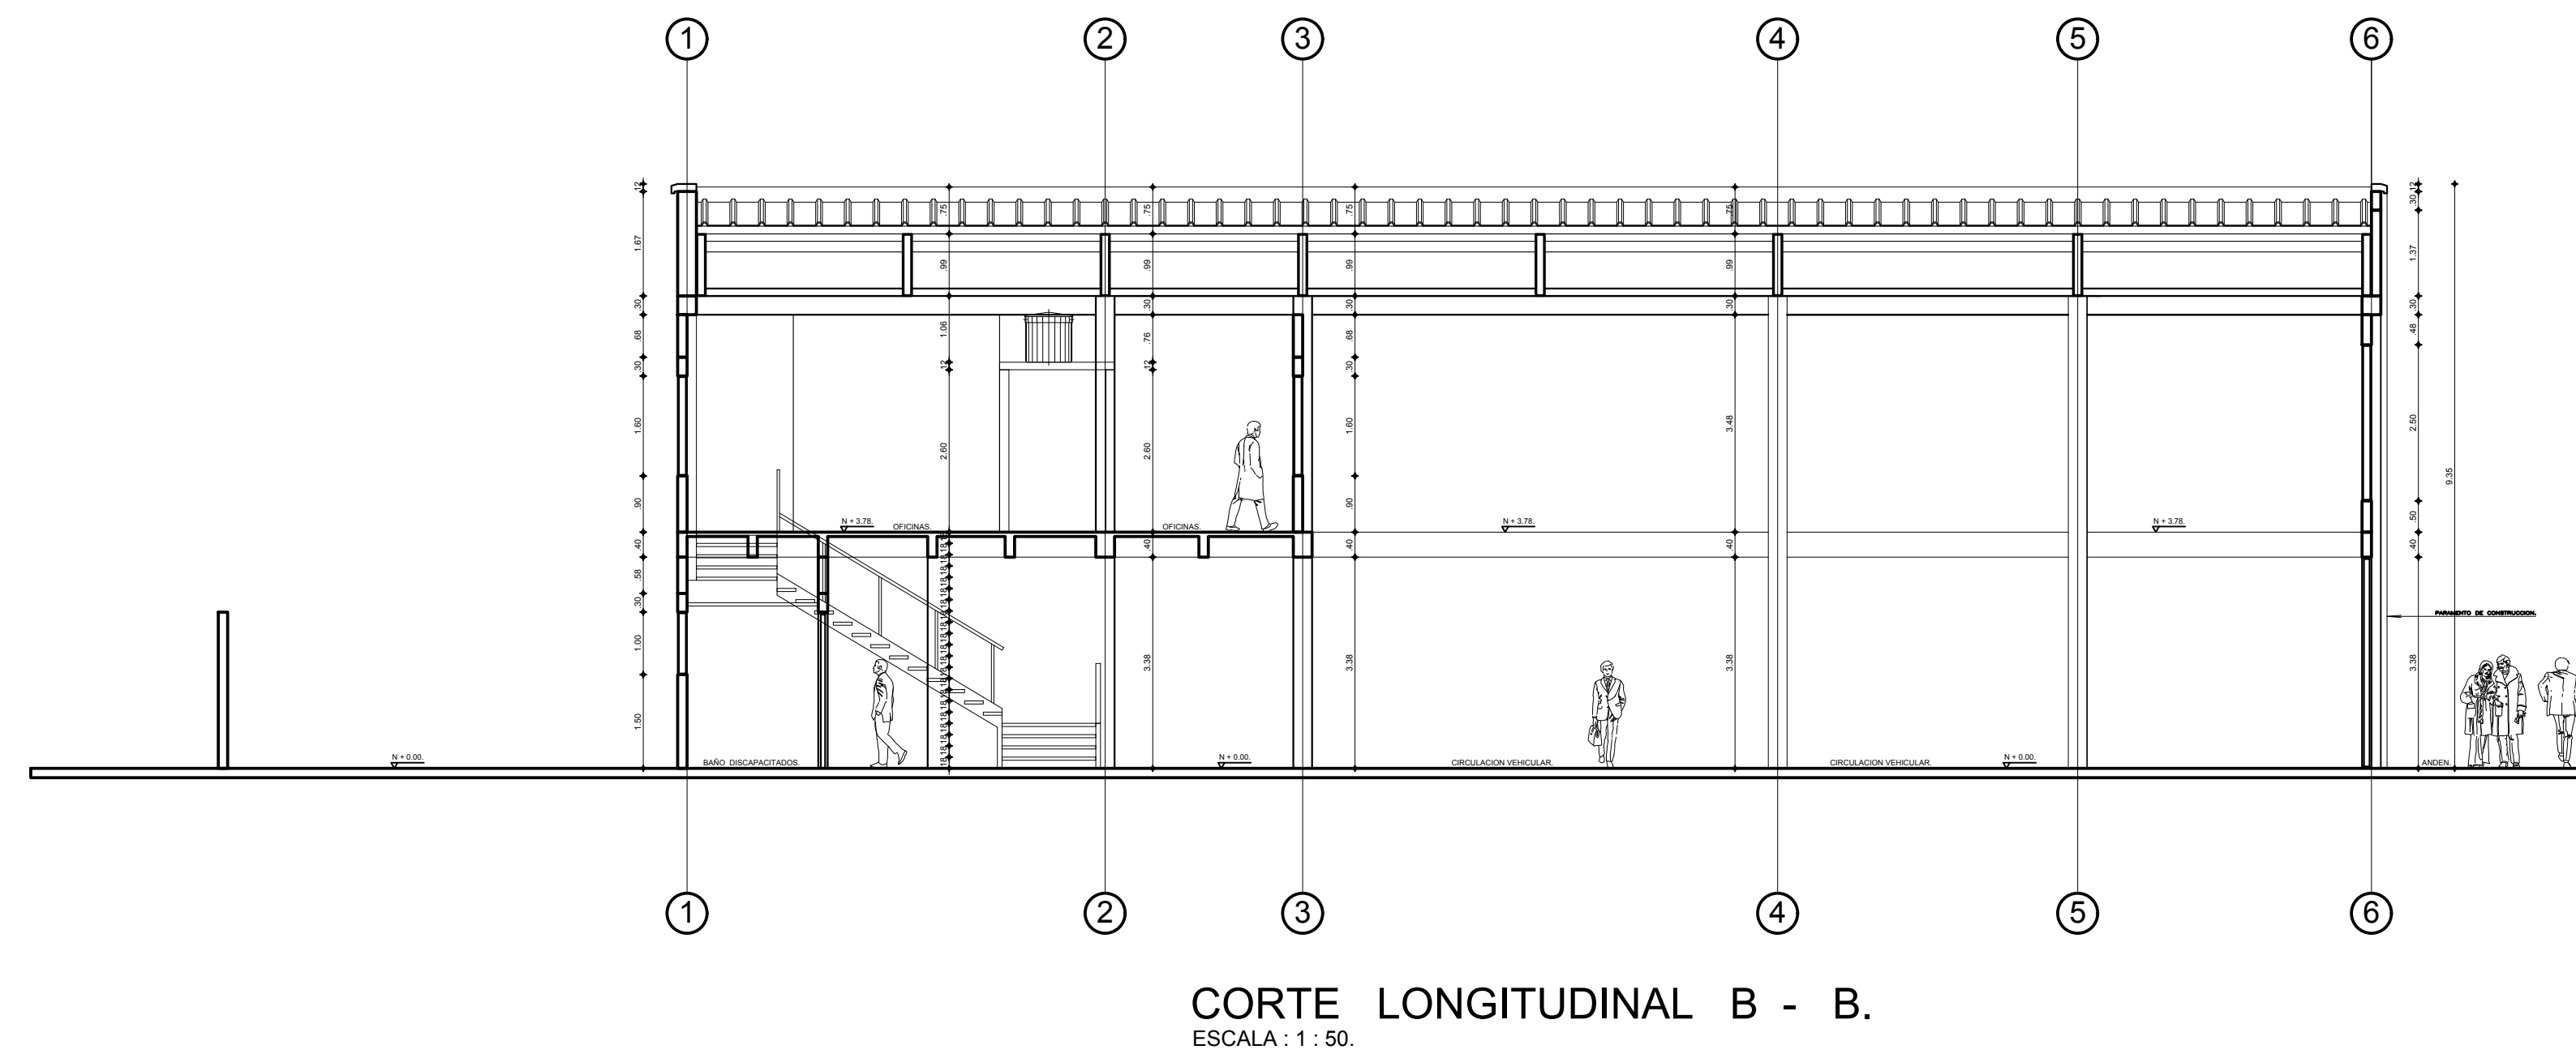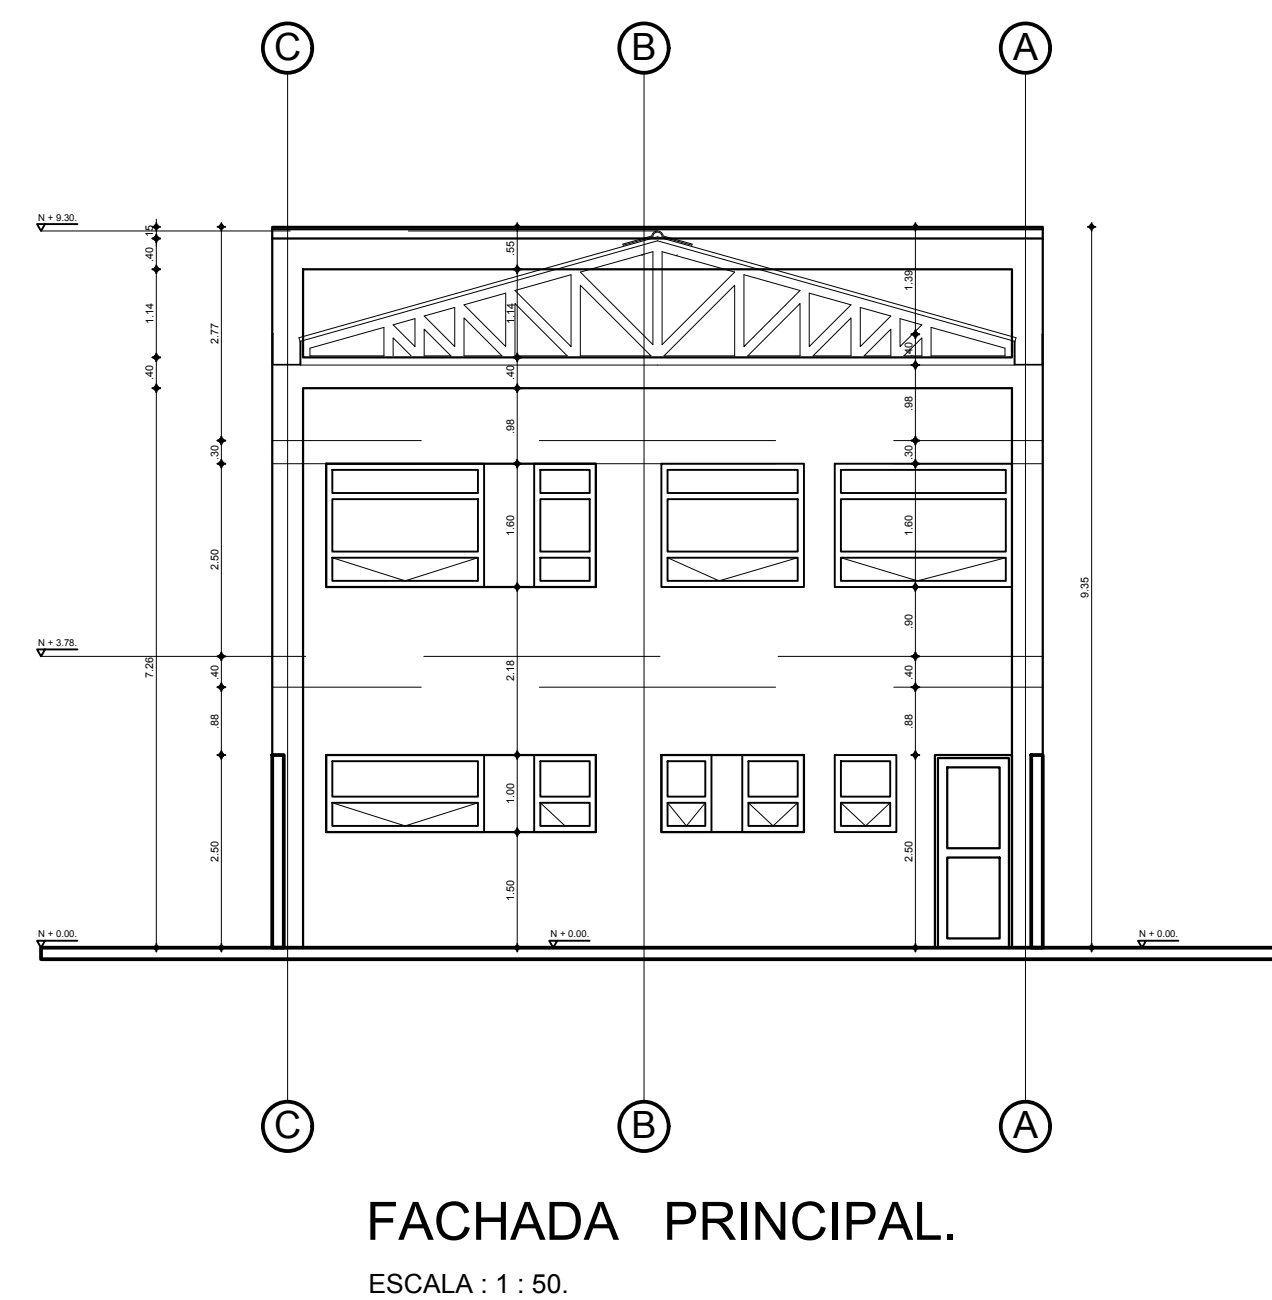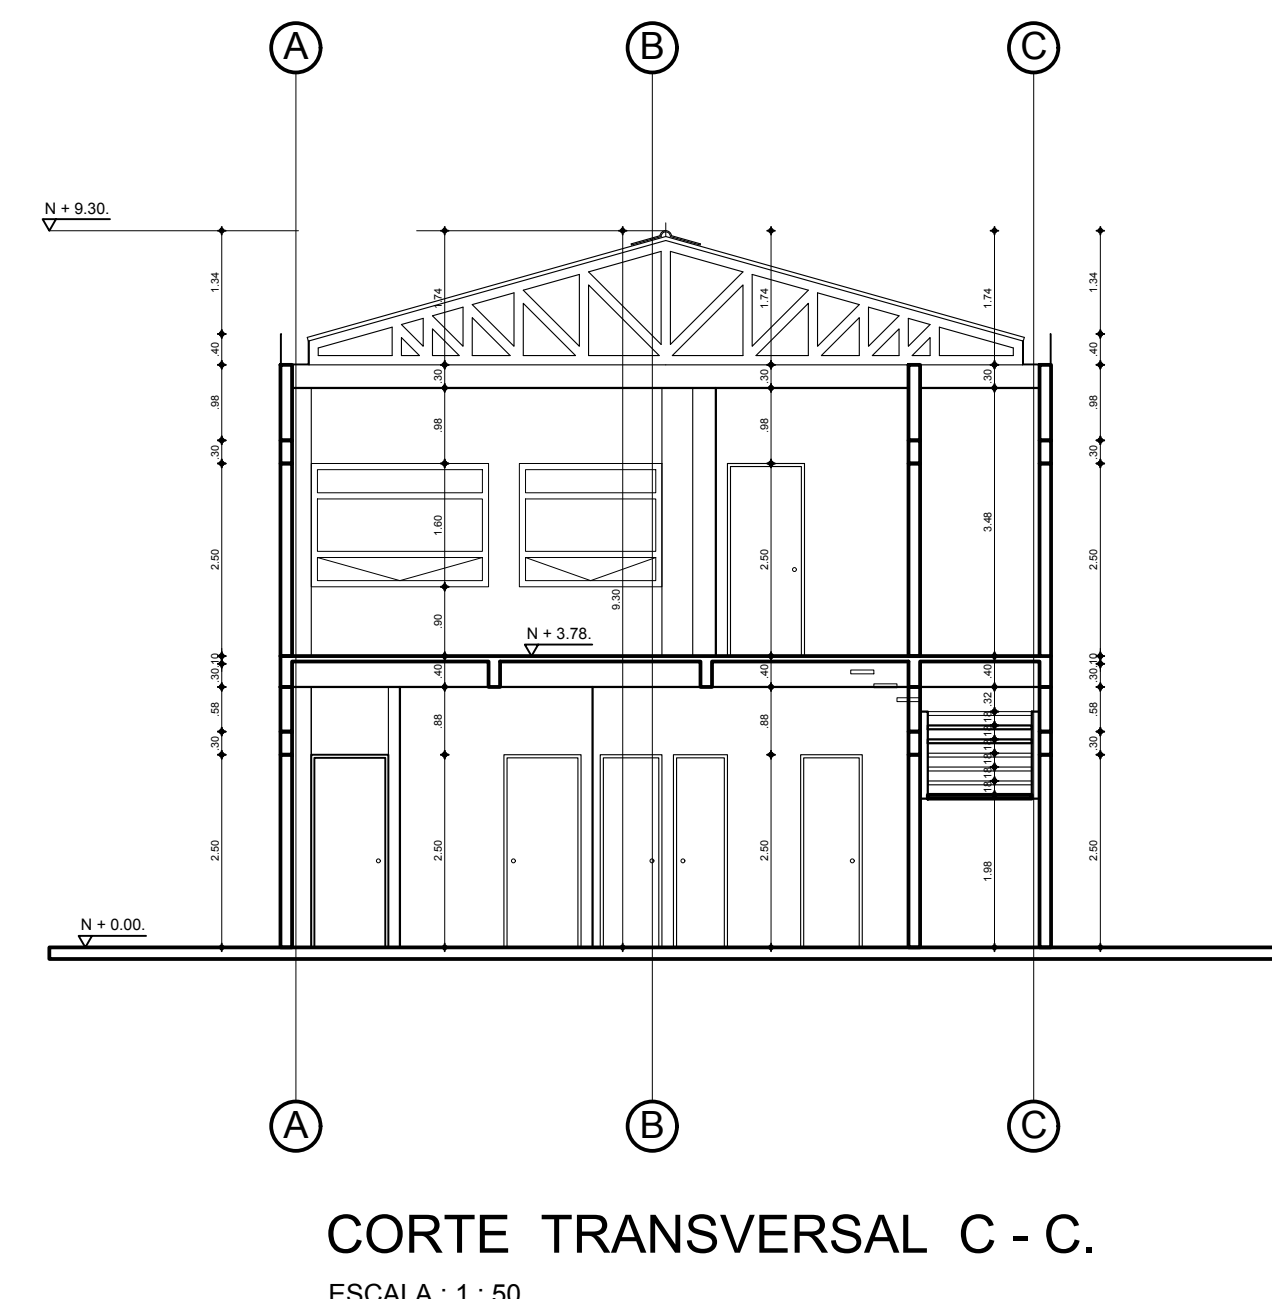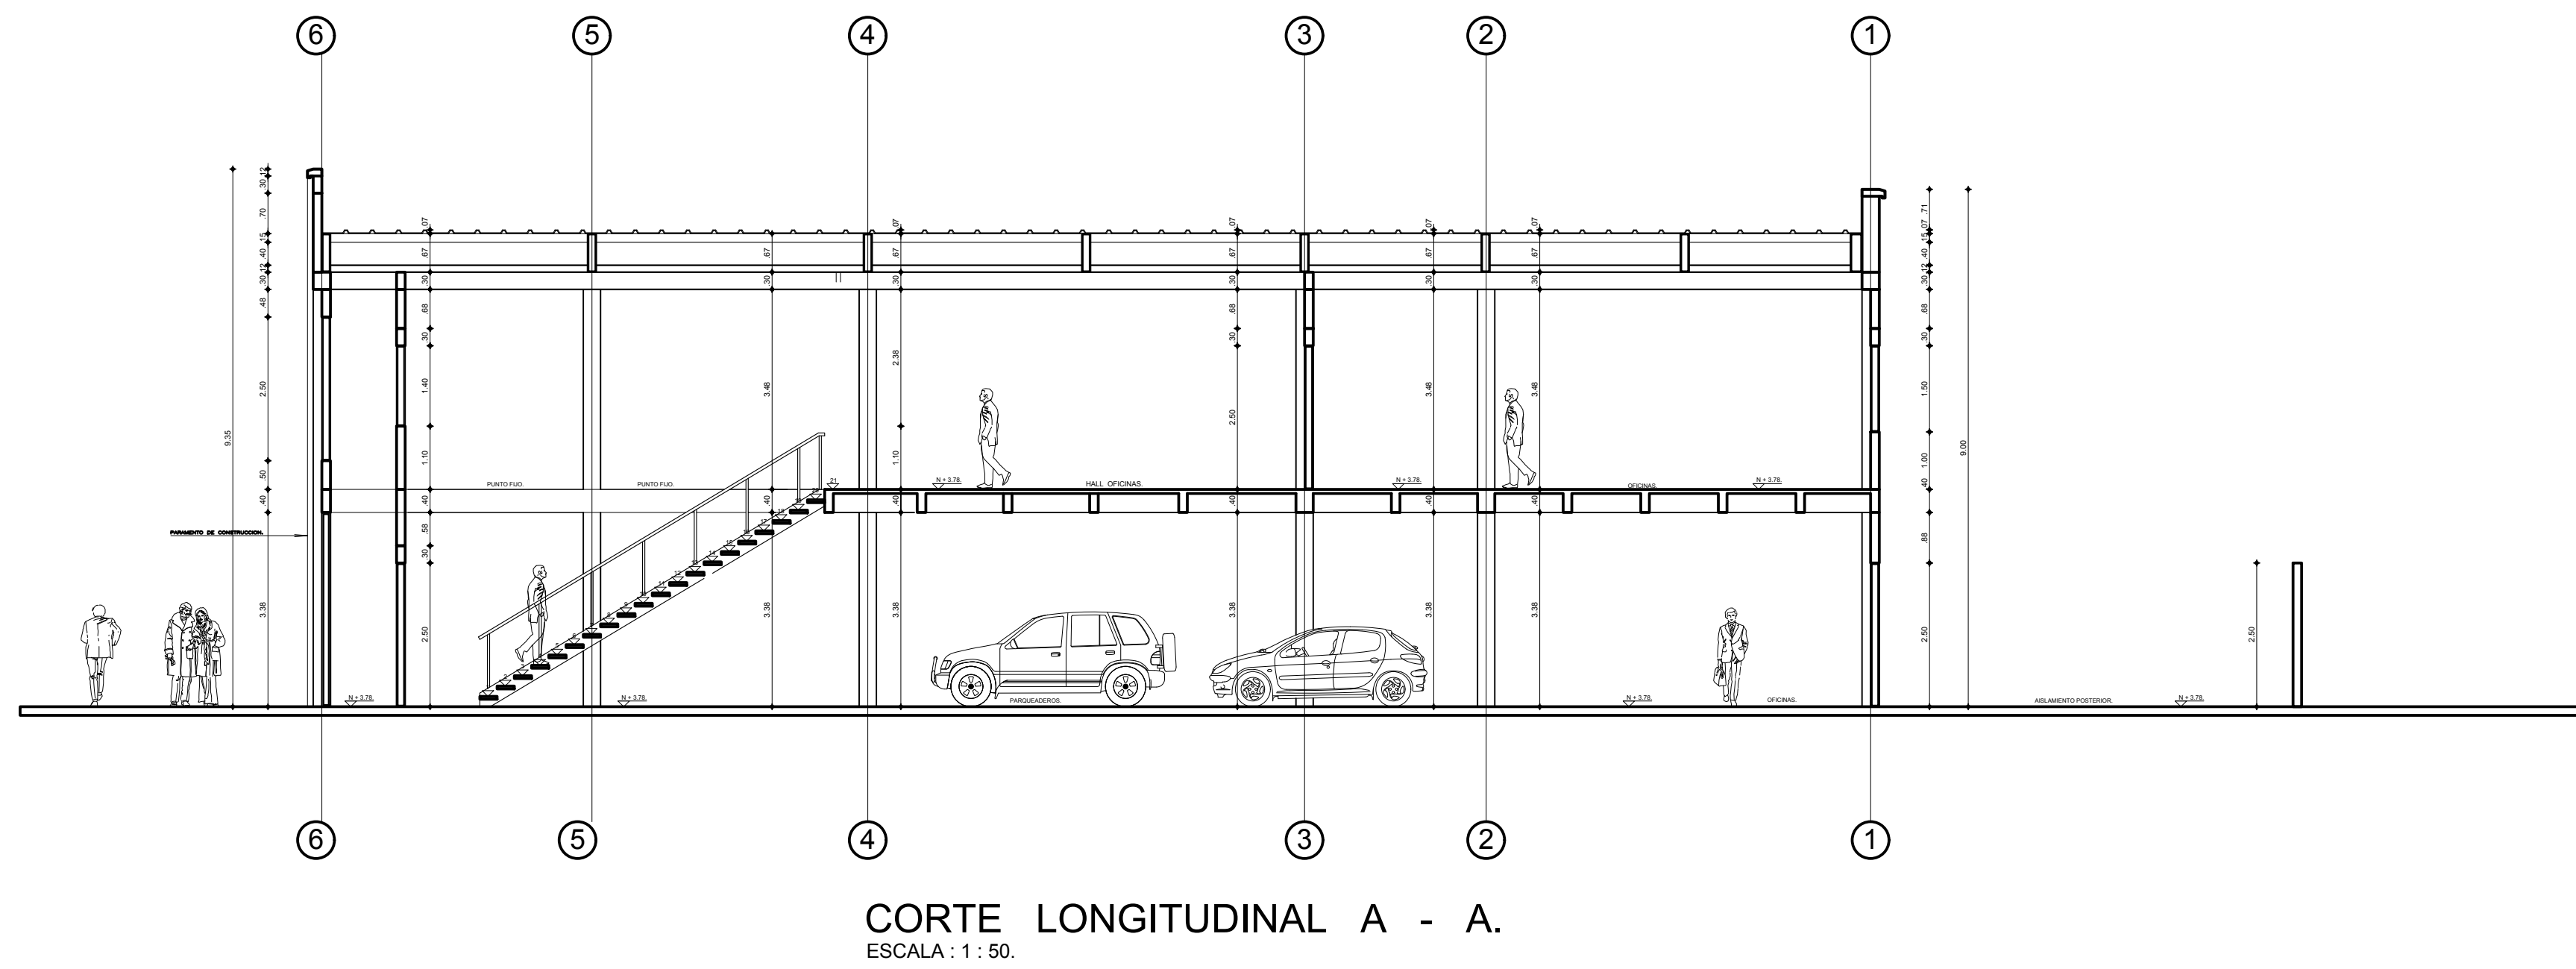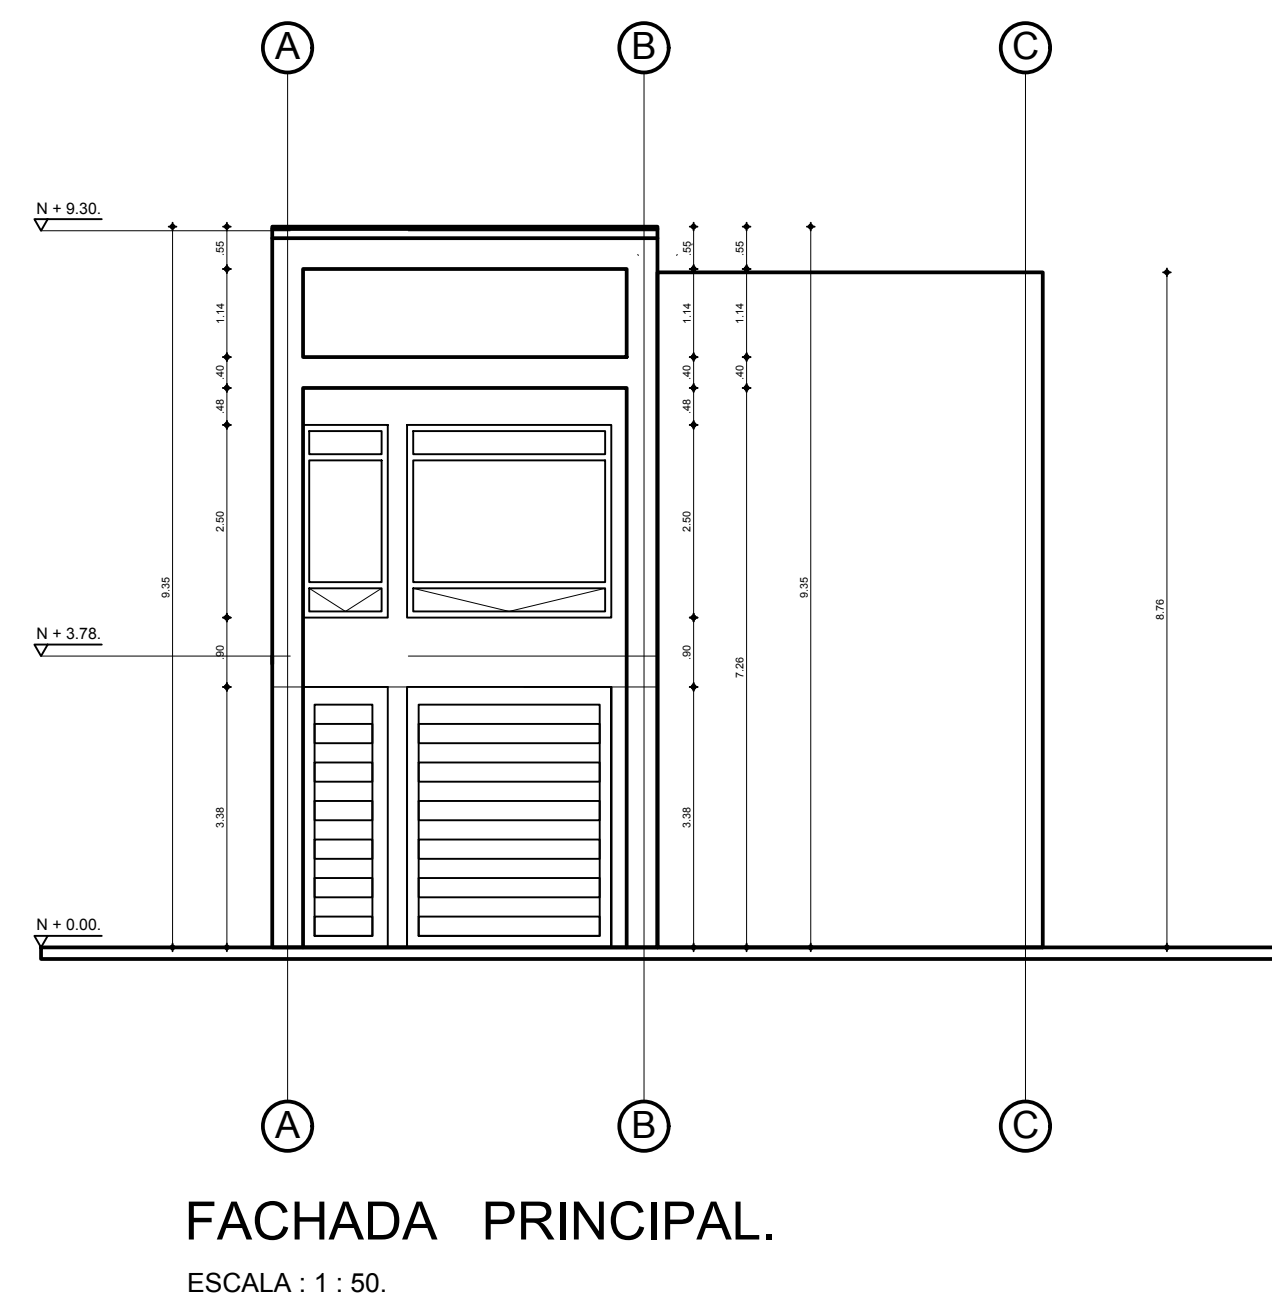



PROYECTO:
**BODEGA
ALCAZARES.**

UBICACION:
CALLE 63 A # 26 - 58.
Barrio Quinta Mutis - Bogotá D.C.


Vº. Bo. PROPIETARIO:

MAGDA RODRIGUEZ CC. 51.837.672 BOGOTÁ PATRICIA RODRIGUEZ CC. 51.777.474 BOGOTÁ.

CONSTRUYE:

CONTIENE
**FACHADA
PRINCIPAL.
POSTERIOR.**

ARQUITECTO RESPONSABLE:
ARQ. JUAN CARLOS GARZON PEDRAZA
MAT. PROF. 25700-37516 CND.

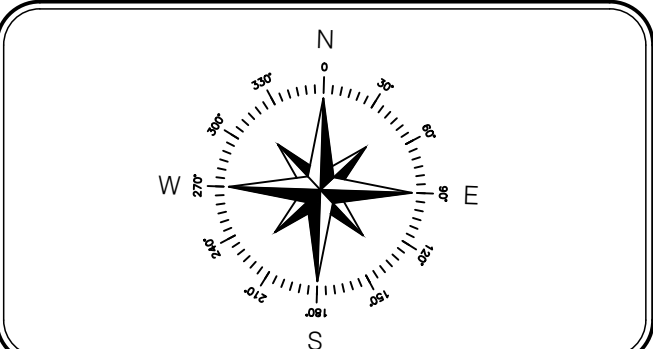

REVISO:

OBSERVACIONES:

SELLOS DE APROBACION:

DIGITO: Samith Taboada email: sstabadag@gmail.com


LINEA DE ACCESO											
D:\Arquitectura\2016\acod_fres\arquitectos\Arq_Garzon\Plano_137-26.dwg											
PLUMAS PARA PLOTEAR											
Color	Plot No	Plot Width	Color	Plot No	Plot Width	Color	Plot No	Plot Width	Color	Plot No	Plot Width
Red	7	0.13	8	7	0.13	9	114	7	0.05		
Yellow	7	0.20	10	7	1.00	120	7	0.45			
Green	7	0.30	11	7	0.70	200	15	7	0.35		
Cyan	7	0.40	15	7	0.15	140	7	0.25			
Blue	7	0.50	30	20	7	0.10	201	7	0.15		
Magenta	7	0.60	44	7	0.10	254	7	0.10			
	7	1.10	45	7	0.45						
	8	0.80	70	7	0.15						

FECHA
22-12-2016


ESCALA
1:50

PLANO No.
A4

DE : **04**

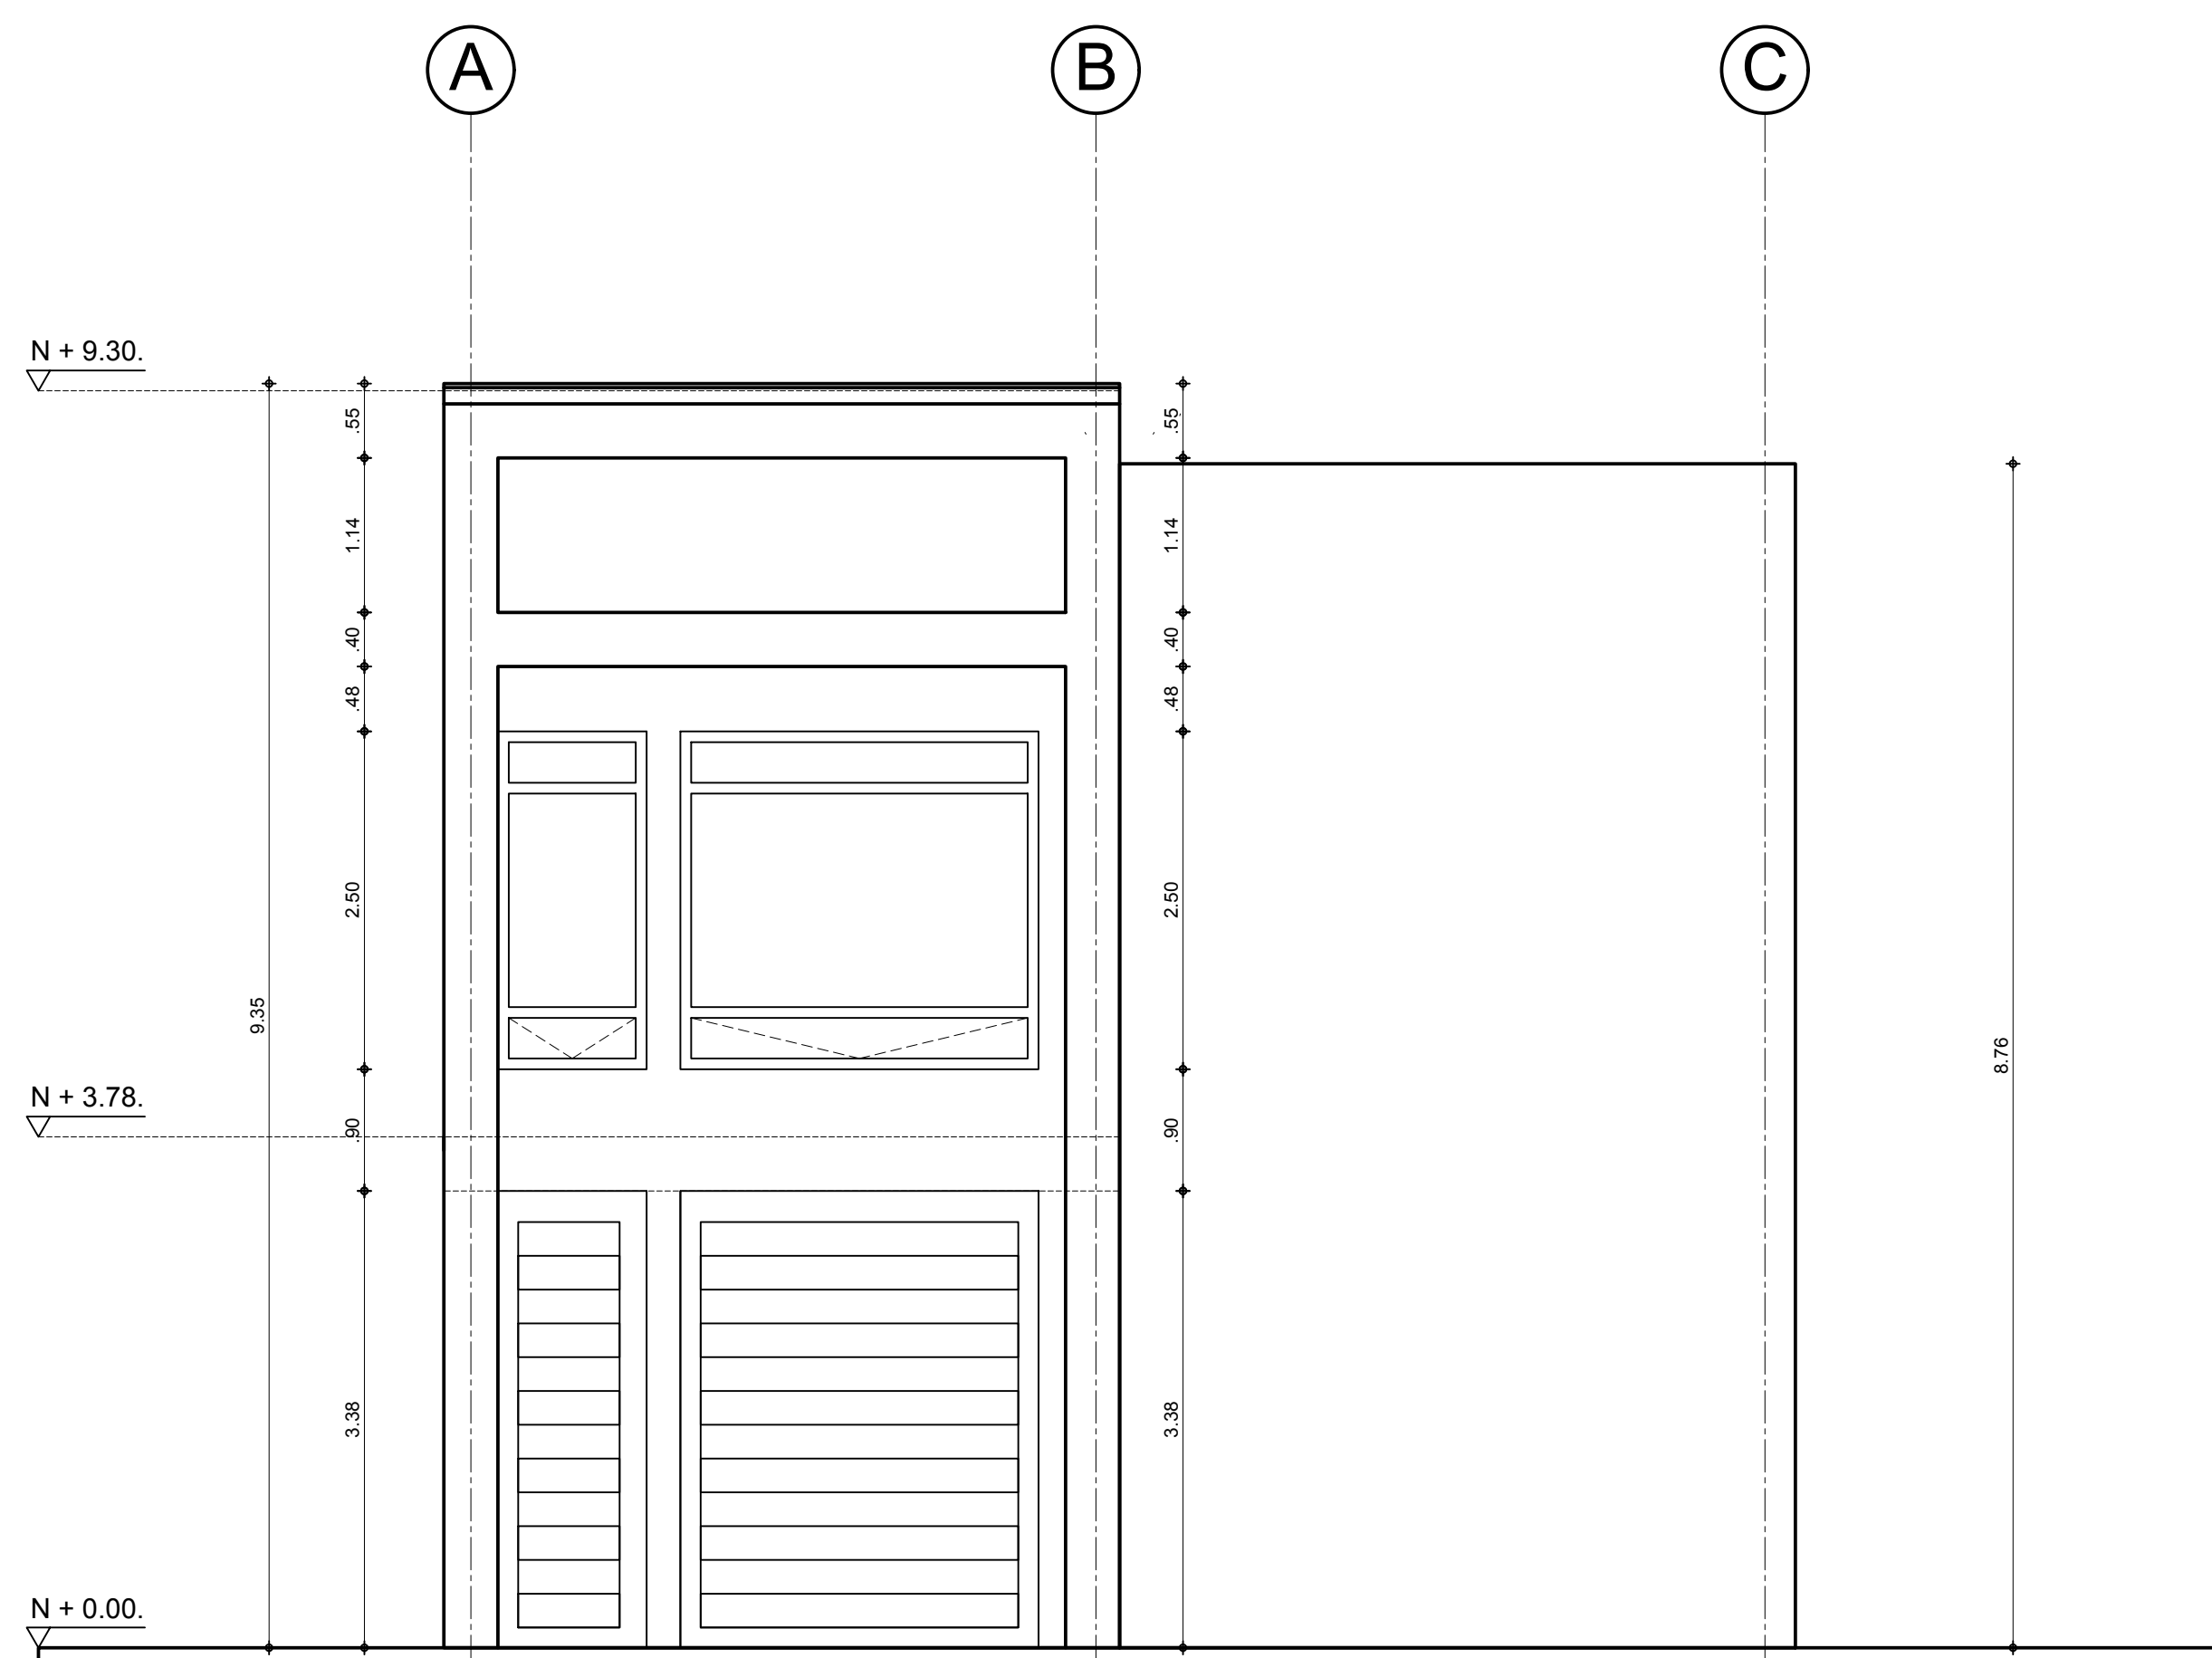

FACHADA PRINCIPAL.
ESCALA : 1 : 50.

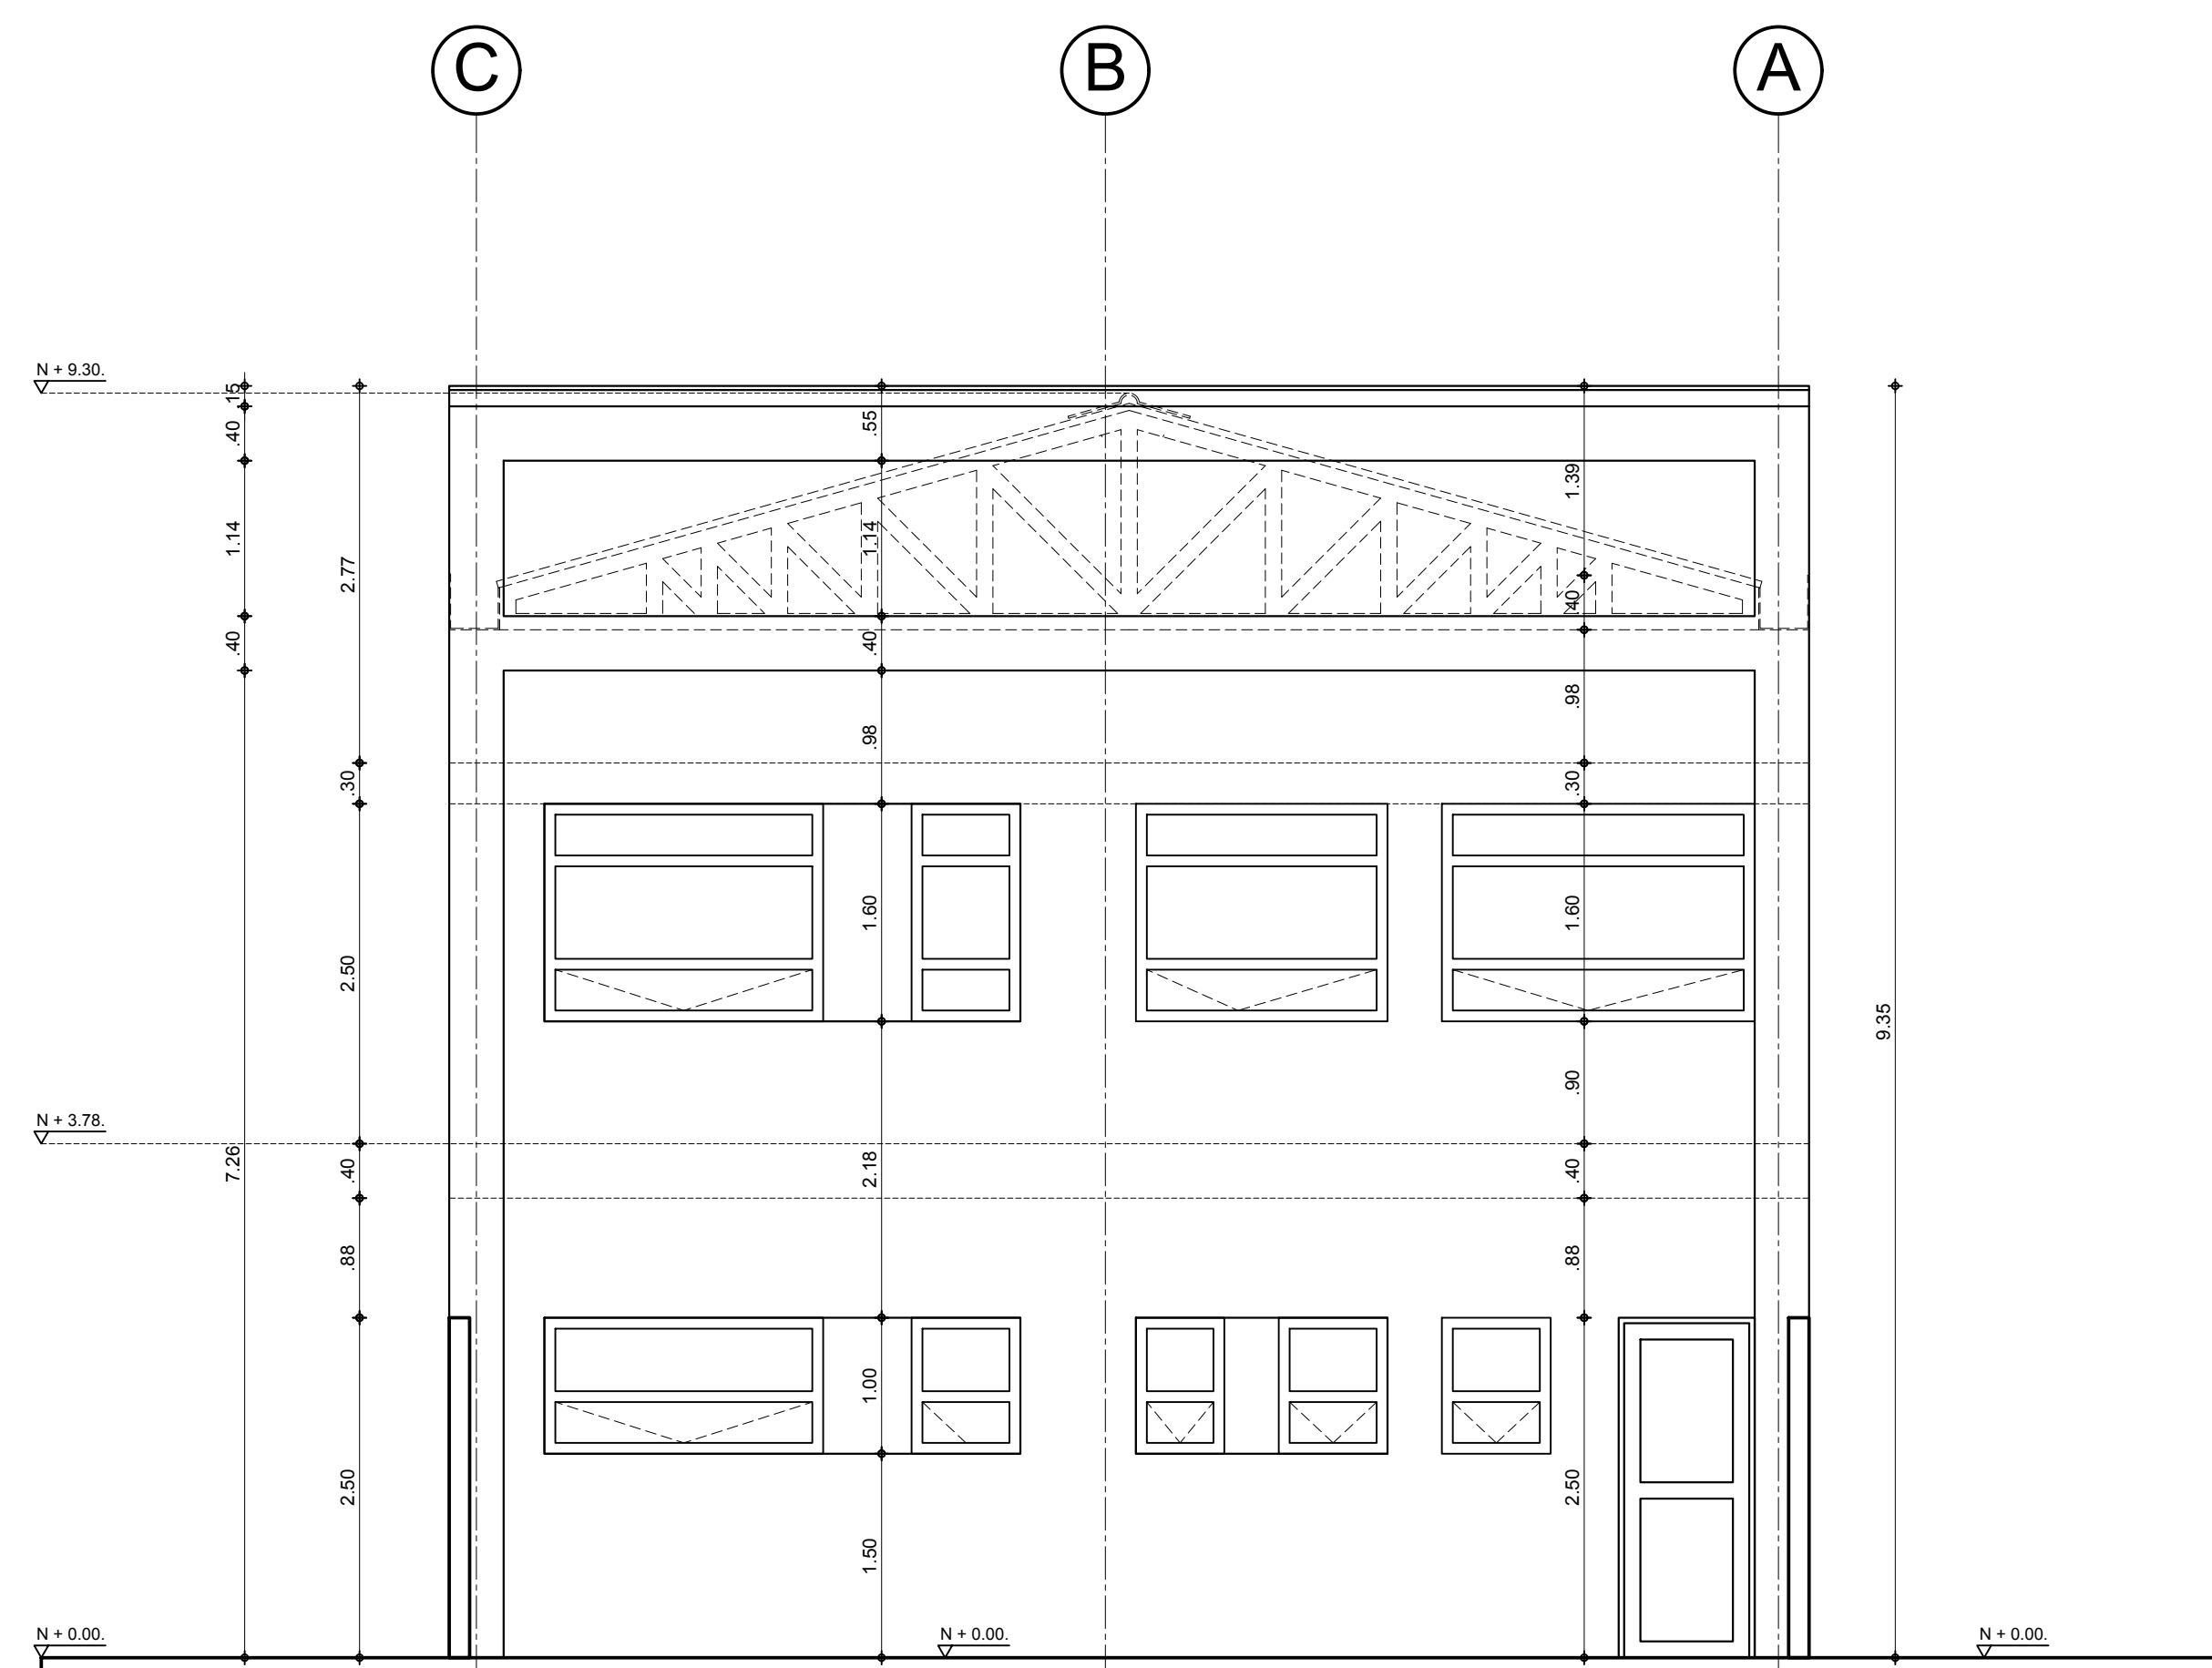

FACHADA PRINCIPAL.
ESCALA : 1 : 50.