



1 PLANTA DE CIMENTACIÓN Y PRIMER PISO

Esquema general de localización de elementos estructurales.

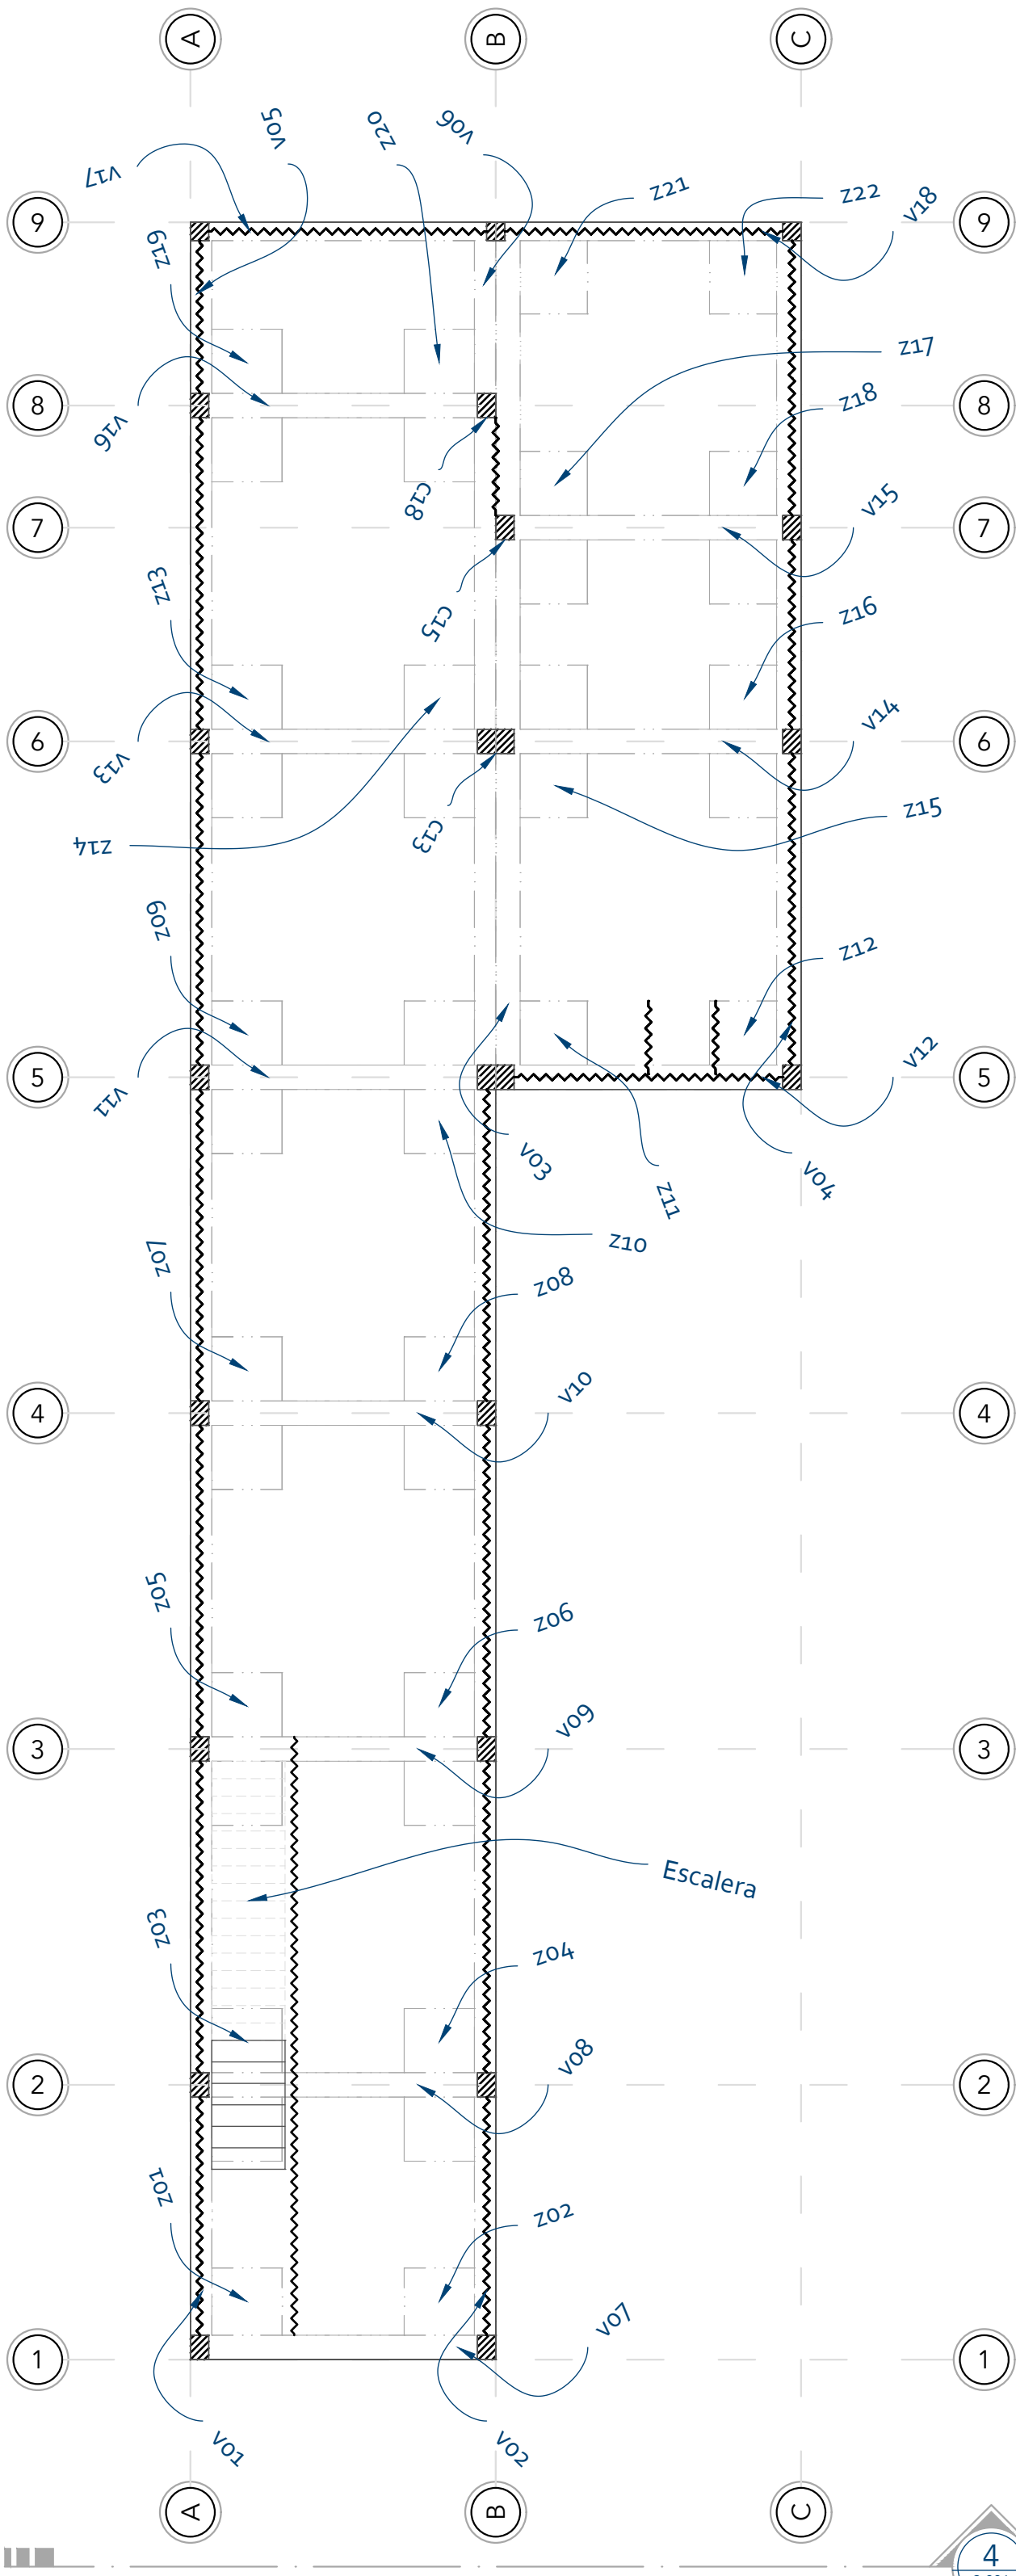


2 PLANTA DE ENTREPISO

Esquema general de localización de elementos estructurales.

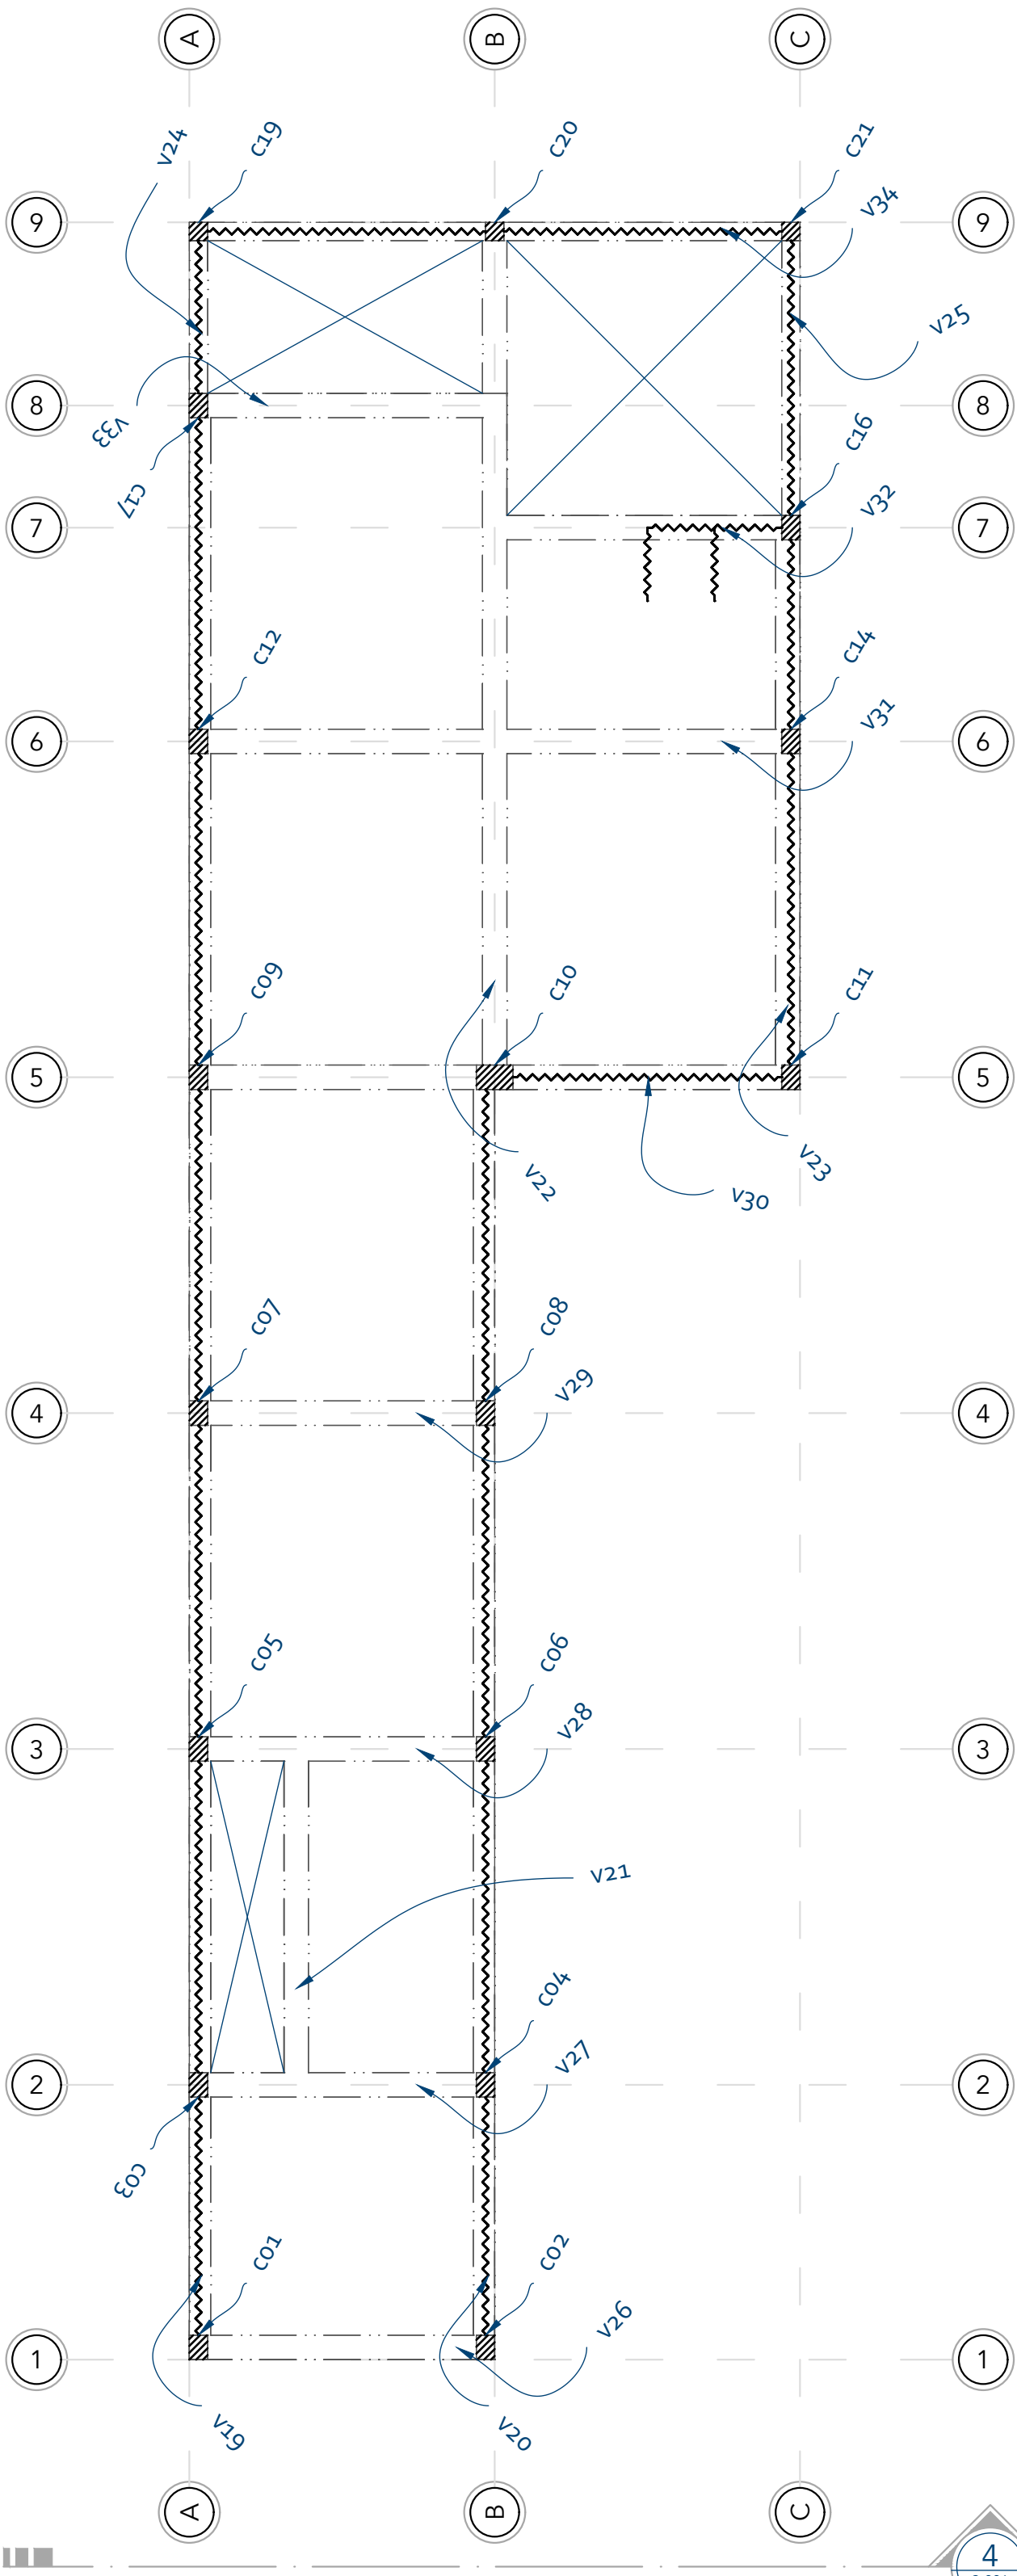


3 PLANTA DE CUBIERTA

Esquema general de localización de elementos estructurales.

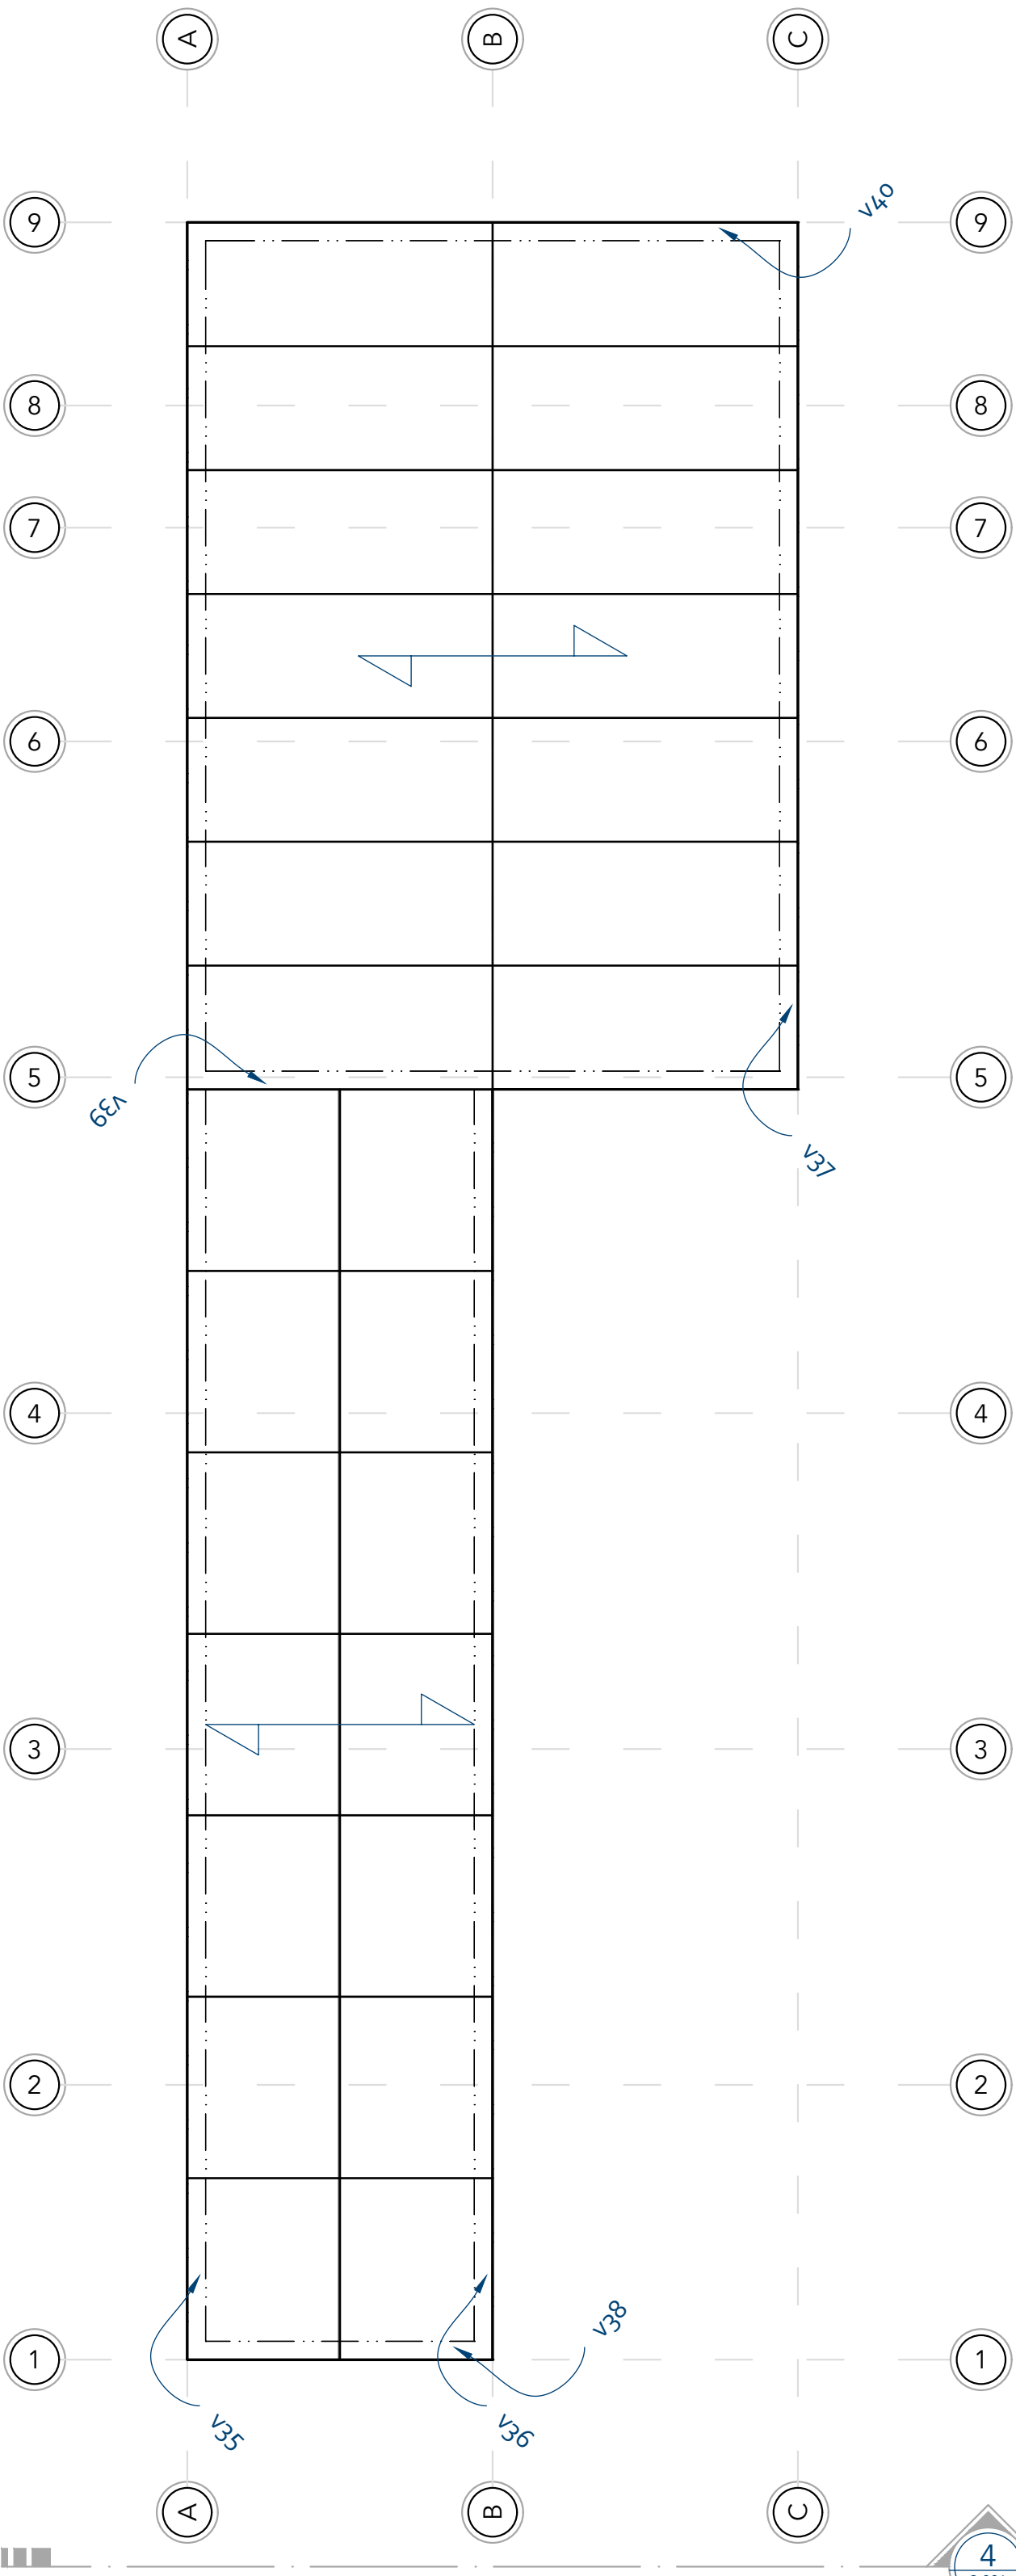

4 ALZADO FRONTAL - FACHADA SUR

Elevación y niveles de estructura.

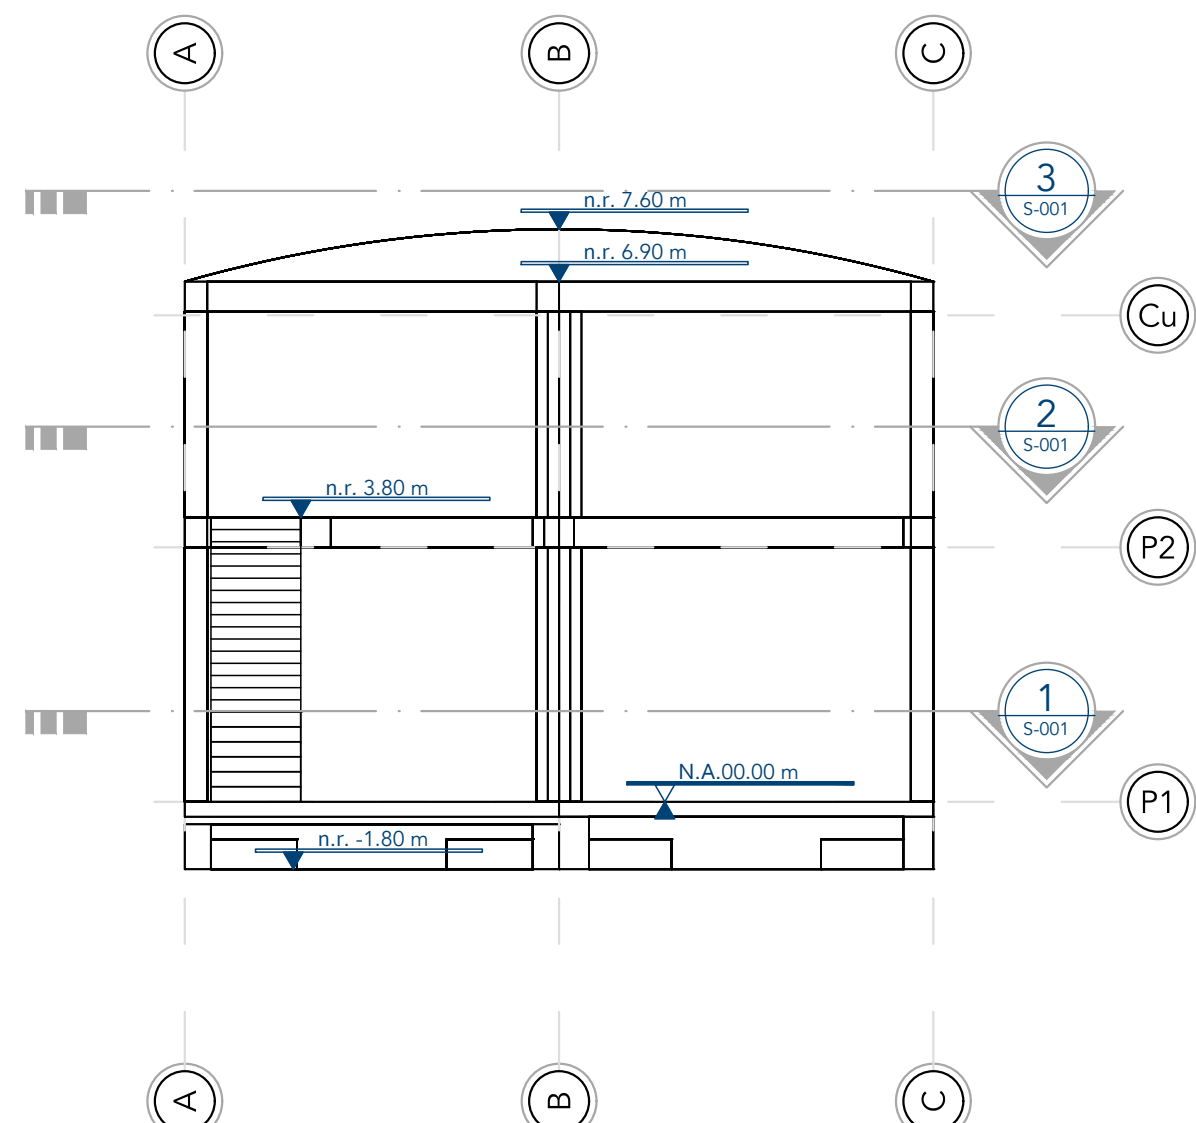

5 RESUMEN DE PROYECTO ESTRUCTURAL

Clasificación y nomenclatura de elementos estructurales en el proyecto.

Elemento	Cantidad	Medida	Comentarios
Vigas	35	384.70	longitud total (m).
V. amarre	15	139.70	múltiples secciones
V. carga	7	156.10	sección cuadrada C3
V. rigidez	12	71.60	sección cuadrada C3
V. auxiliar	1	17.30	múltiples secciones
Losas	3	454.40	área construida total (m²).
L. contrapiso	2	246.00	losas macizas
L. entepiso	1	208.40	losa aligra en una dirección

Elemento	Cantidad	Medida	Comentarios
Columnas	21	121.80	longitud total (m).
C. esquinera	5	31.00	sección tipo C2
C. medianera	13	75.00	sección tipo D2
C. central	3	15.80	sección tipo EX
Zapatas	22	99.73	área de terreno (m²)
Z. esquinera	6	15.75	sección cuadrada C10
Z. medianera	16	83.98	sección rectangular R10:2
Cubierta	1	248.00	área construida total (m²).

Elemento	Cantidad	Medida	Comentarios
Muros	48	1221.36	área construida total (m²).
M. perimetral	35	1093.60	
M. divisorio	10	90.36	
M. acceso	3	37.40	
Otros (no est.)	—	—	
Escalera	1	7.69	longitud total (m).
Soporte tanques	1	0.10	

Resumen de proyecto estructural

Edificación comercial con sistema estructural aporticado en concreto reforzado; muros y divisiones en mampostería sismo-resistente; cimentación a base de zapatas armadas.

+ Construcción total:	702.40 m² (≈1 984 m³)
+ Volumen de concreto:	≈ 115.50 m³
+ Acero estimado:	≈ 71 465.50 kg
+ Peso total de edificación:	≈ 380.50 ton

CUADRO DE CONVENCIONES	
Marcas de identificación de elementos	
	Columnas
	Vigas
	Zapatas
	Direcciones de drenaje
	Vacios estructurales
	Muros estructurales
	Dibujo en primer plano
	Dibujo en segundo plano
	Dibujo en plano de fondo
	Dibujo en proyección

Diseño y dibujo
I.C. JUAN C. TORRES CEDANO
Revisión y aprobación
Proprietario, contratista o cliente de proyecto

FAMILIA RODRIGUEZ
Magda L. Rodríguez

Información de proyecto

BODEGA RODRIGUEZ
Revisión de diseños

Título y contenido de la hoja

Proyecto estructural para edificación.


ID de proyecto
COA0000d/0a
Escala
1 : 100

Número ID de la hoja
S-001

Este documento y su contenido son propiedad de Corporación Nacional de Trabajo, Desarrollo e Innovación Profesional para el sector privado. Cualquier uso, reproducción o explotación de este material sin consentimiento escrito, por parte de cualquier entidad, será sancionado legalmente. — Original publicado bajo licencia Creative Commons CC BY-SA 4.0

PLANTA DE NIVEL DE CUBIERTA

Dimensiones principales de elementos estructurales y distancias constructivas.

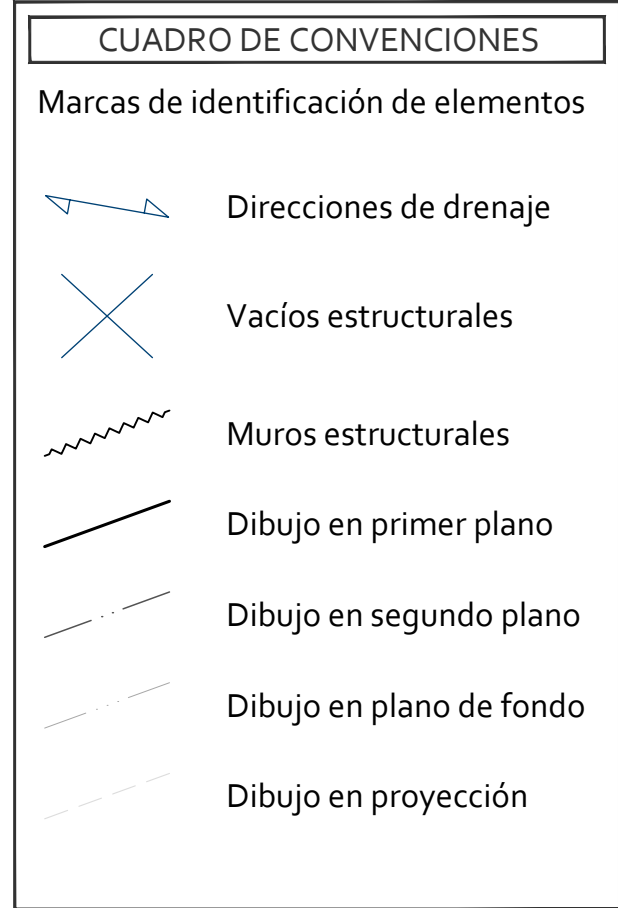

NOTA:
PLANO PROVISIONAL SUJETO A REVISIÓN Y MODIFICACIÓN. NO APROBADO PARA CONSTRUCCIÓN



 ESTUDIO C PROYECTOS S de RL de CV	
Diseño y dibujo I. C. JUAN C. TORRES CEDANO	
Revisión y aprobación	
Propietario, contratista o cliente de proyecto	
FAMILIA RODRIGUEZ Magda L. Rodríguez	
Información de proyecto	
BODEGA RODRIGUEZ Revisión de diseños	
Título y contenido de la hoja	
Planta estructural de cubierta.	
Id de proyecto COA0000d/oa	Número Id de la hoja S-004
Escala 1 : 50	
Este documento y su contenido son propiedad de Corporación Nacional de Trabajo, Desarrollo e Innovación Profesional y no son otorgados, cedidos, en distribución ni reproducción de ningún material sin consentimiento por escrito del titular de todos los derechos de la obra intelectual, será sancionado legalmente. — Original publicada bajo licencia Creative Commons CC BY-SA 4.0	